CASA MORIYAMA

Ryue Nishizawa (SANAA) · Ota-ku, Tokio · 2002-2005

Vivienda del propietario + 5 apartamentos de alquiler, repartidos en 10 cajas independientes (A-J) de muros de chapa de acero.
Parcela ~290 m² (publicada) · superficie construida ~263 m² · muros de 6 cm · cajas de 1 a 3 plantas con sótanos y semisótanos puntuales.

Caja	Uso por planta	Planta (m)	Pl.	Niveles de suelo FL	Alturas libres h.l.	Cubierta	Fuente altura
A	Salón / Estudio / almacén (techo bajo) / Dormitorio-estudio	5,63 × 4,03	3	+0,10 / +2,45 / +4,47	2,20 / 1,87 / 3,10	+7,87	Axonometría
B	Cocina-comedor / Dormitorio	3,03 × 1,83	2	+0,05 / +2,30	2,10 / 2,42	+5,02	Sección original
C	Estudio-salón	2,73 × 4,03	1	+0,60	2,54	+3,64	Sección original
D	Baño	1,81 × 1,25	1	+0,05	1,90	+2,07	Sección original
E	Cocina-comedor / Dormitorio	3,18 × 2,73	2	+0,05 / +2,30	2,10 / 2,43	+5,03	Sección original
F	Salón-comedor-cocina / Dormitorio + baño / Estudio	3,78 × 5,03	3	+0,05 / +2,70 / +5,15	2,50 / 2,30 / 2,42	+7,87	Sección original
G	Salón (semisótano)	4,43 × 4,43	1	-0,41	2,19	+2,09	Sección original
H	Baño (de G)	2,33 × 1,35	1	±0,00	3,71	+4,02	Sección original
I	Salón-dormitorio	4,78 × 4,28	1	+0,10	4,35	+4,84	Sección original
J	Salón-dormitorio + baño	2,88 × 5,38	1	+0,10	2,84	+3,34	Axonometría

PLANOS


01 Emplazamiento y cubiertas
02 Planta baja
03 Planta primera
04 Planta segunda
05 Alzados sur y norte
06 Alzados este y oeste
07 Secciones A-A y B-B
08 Secciones C-C y D-D
09 Sección D-D 1:50 (B y A)
10 Sección C-C 1:50 (F y G)
11 Axonometrías
12 Imágenes (renders Revit)

NOTAS

Cotas de planta: planta baja original de la oficina de R. Nishizawa (cotas por caja).
Alturas: secciones constructivas originales (B-D-I y C-G-H) y axonometría, medidas a escala (±0,10-0,20 m).
Forjados intermedios (0,15) y algunos huecos de las fachadas norte y oeste: hipótesis razonadas (maqueta 1:50 del MoMA).
Muros: chapa de acero estructural con aislamiento y acabado interior, espesor total 6 cm.
Origen de coordenadas: cara oeste de E/F y cara sur de H/I. Rasante ±0,00. Norte según planta original.

CASA MORIYAMA
Ryue Nishizawa (SANAA) · Ota-ku, Tokio · 2002-2005 · Levantamiento

PLANO	ESCALA	
ÍNDICE Y DATOS	-	
PROYECTO BASE · H2 · Grupo X Fecha: octubre 2026 · Cotas en metros	Nº **00**	A3

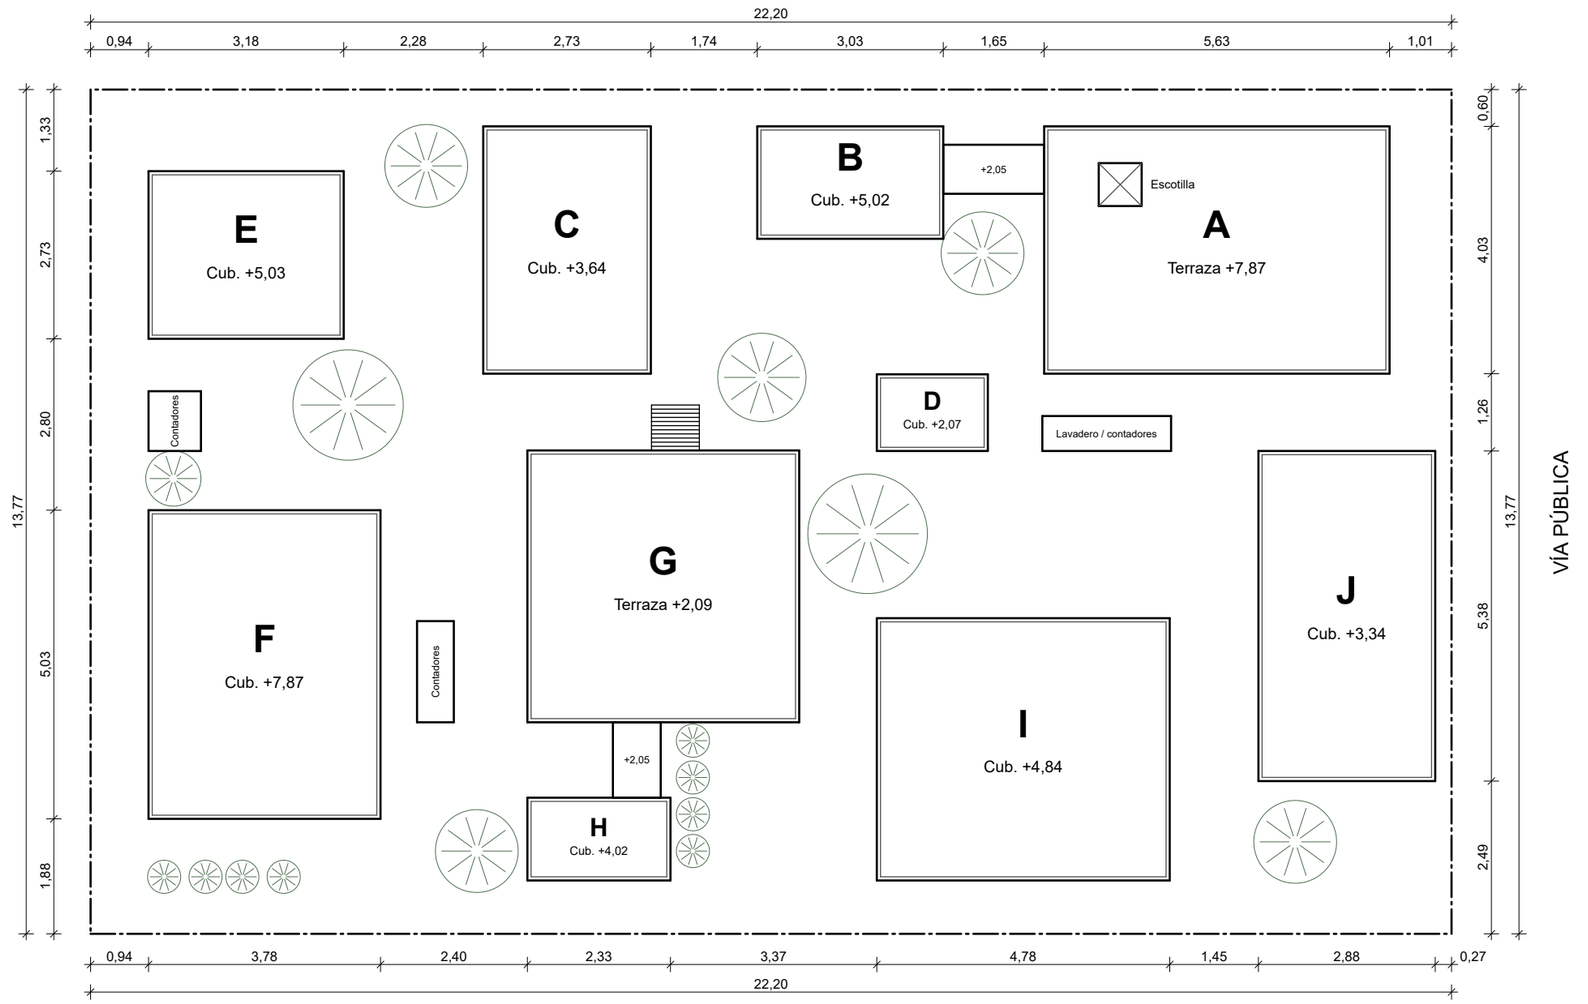

EMPLAZAMIENTO Y CUBIERTAS E 1:100


VÍA PÚBLICA

Muro: chapa de acero + aislamiento, e = 0,06 m
h.l. = altura libre · FL = nivel de suelo
Cotas en metros
Parcela aprox. 22,20 × 13,77 m (publicada 290 m²)

CASA MORIYAMA

Ryue Nishizawa (SANAA) · Ota-ku, Tokio · 2002-2005 · Levantamiento

PLANO	ESCALA	
EMPLAZAMIENTO Y CUBIERTAS	**1:100**	
PROYECTO BASE · H2 · Grupo X Fecha: octubre 2026 · Cotas en metros	Nº **01**	A3

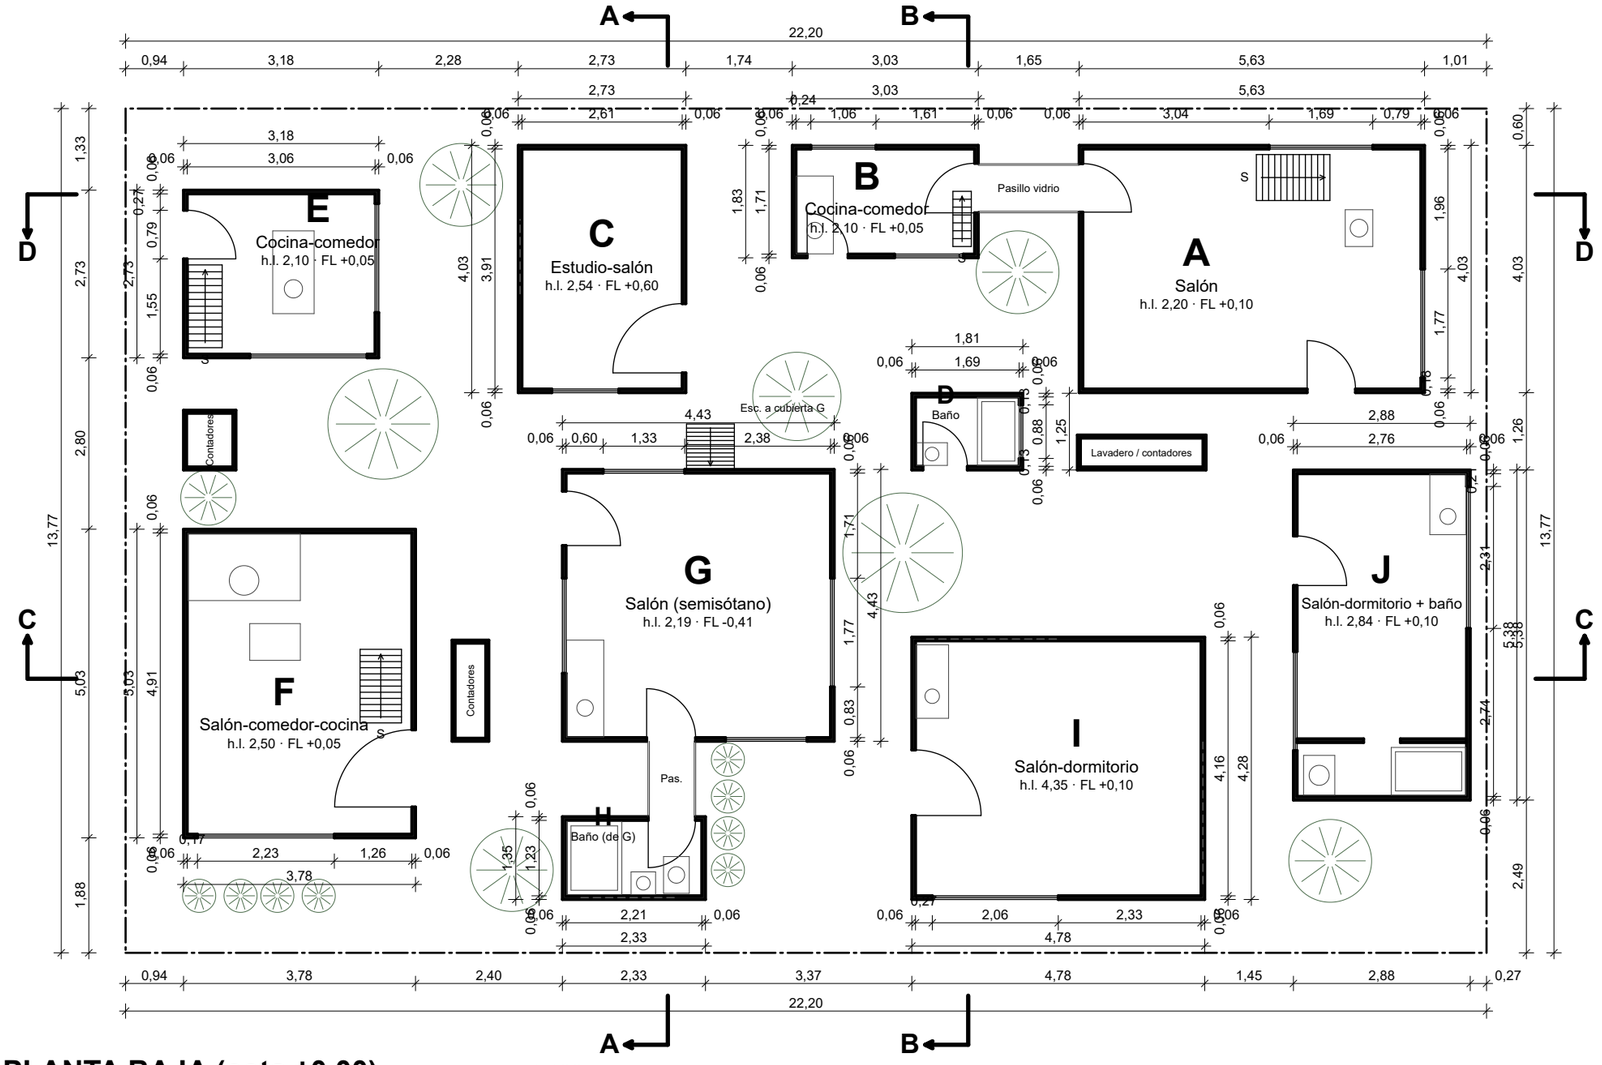

PLANTA BAJA (cota ±0,00)


E 1:100

Muro: chapa de acero + aislamiento, e = 0,06 m
h.l. = altura libre · FL = nivel de suelo
Cotas en metros
Plano de corte +1,20 m · ventanas altas en trazo discontinuo

CASA MORIYAMA

Ryue Nishizawa (SANAA) · Ota-ku, Tokio · 2002-2005 · Levantamiento

PLANO	ESCALA	
PLANTA BAJA	**1:100**	
PROYECTO BASE · H2 · Grupo X Fecha: octubre 2026 · Cotas en metros	Nº **02**	A3

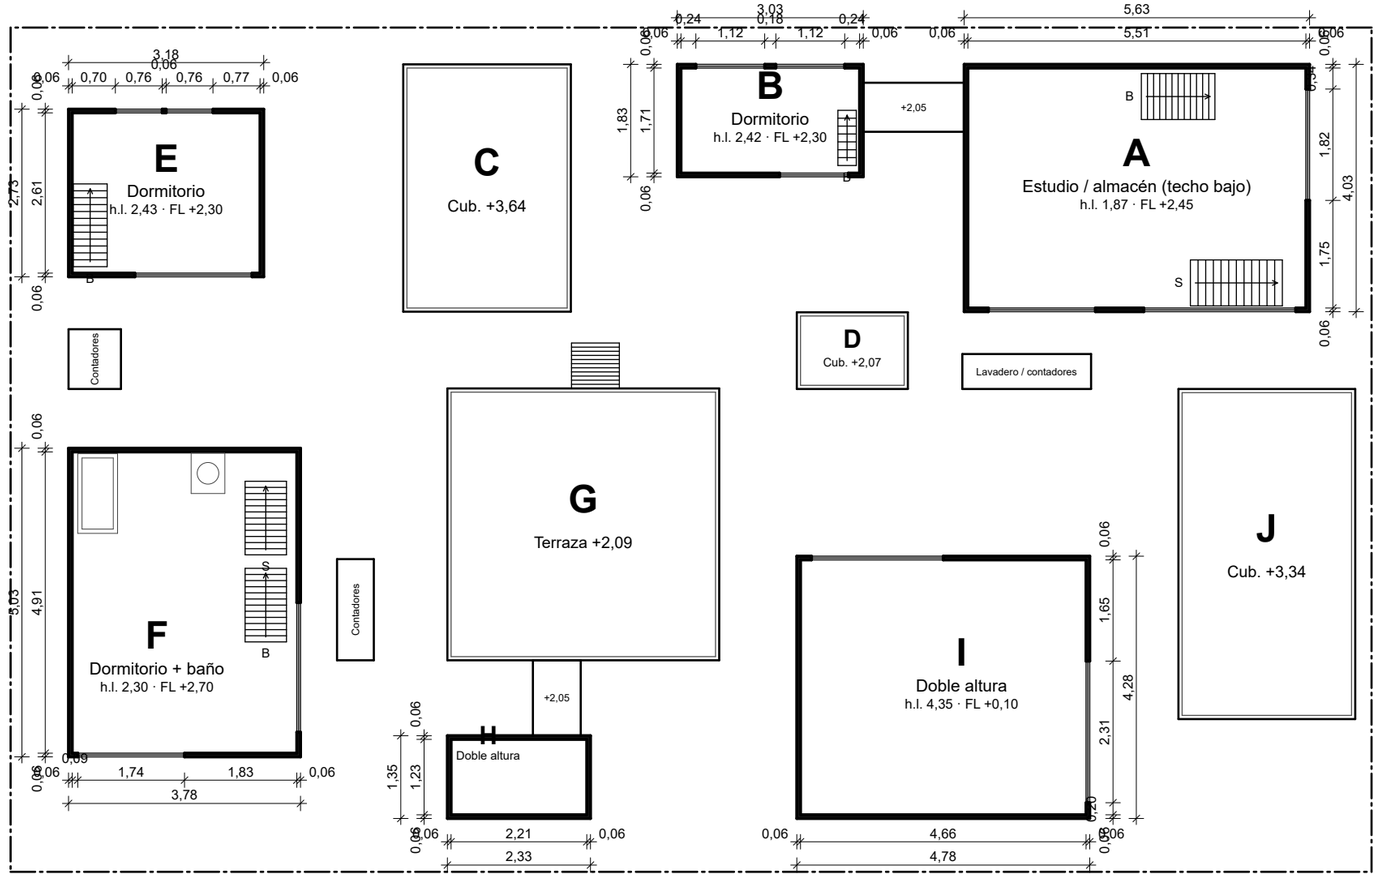

PLANTA PRIMERA E 1:100


Muro: chapa de acero + aislamiento, e = 0,06 m
h.l. = altura libre · FL = nivel de suelo
Cotas en metros
Plano de corte +3,80 m · resto de cajas en cubierta

CASA MORIYAMA

Ryue Nishizawa (SANAA) · Ota-ku, Tokio · 2002-2005 · Levantamiento

PLANO	ESCALA	
PLANTA PRIMERA	**1:100**	
PROYECTO BASE · H2 · Grupo X Fecha: octubre 2026 · Cotas en metros	Nº **03**	A3

N

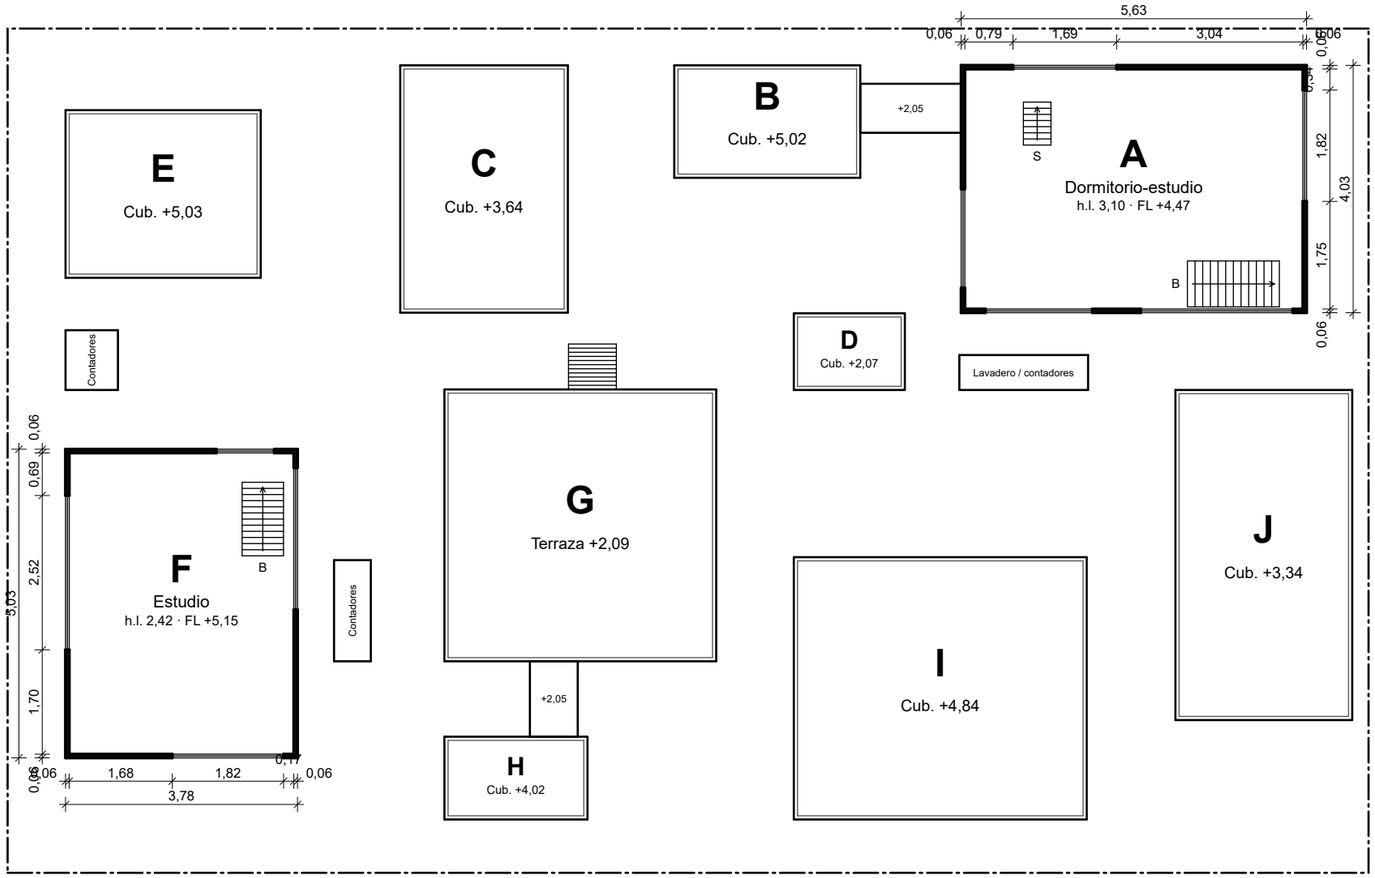


PLANTA SEGUNDA E 1:100

Muro: chapa de acero + aislamiento, e = 0,06 m
h.l. = altura libre · FL = nivel de suelo
Cotas en metros
Plano de corte +6,20 m (cajas A y F)


CASA MORIYAMA

Ryue Nishizawa (SANAA) · Ota-ku, Tokio · 2002-2005 · Levantamiento

PLANO	ESCALA	
PLANTA SEGUNDA	**1:100**	
PROYECTO BASE · H2 · Grupo X Fecha: octubre 2026 · Cotas en metros	Nº **04**	A3

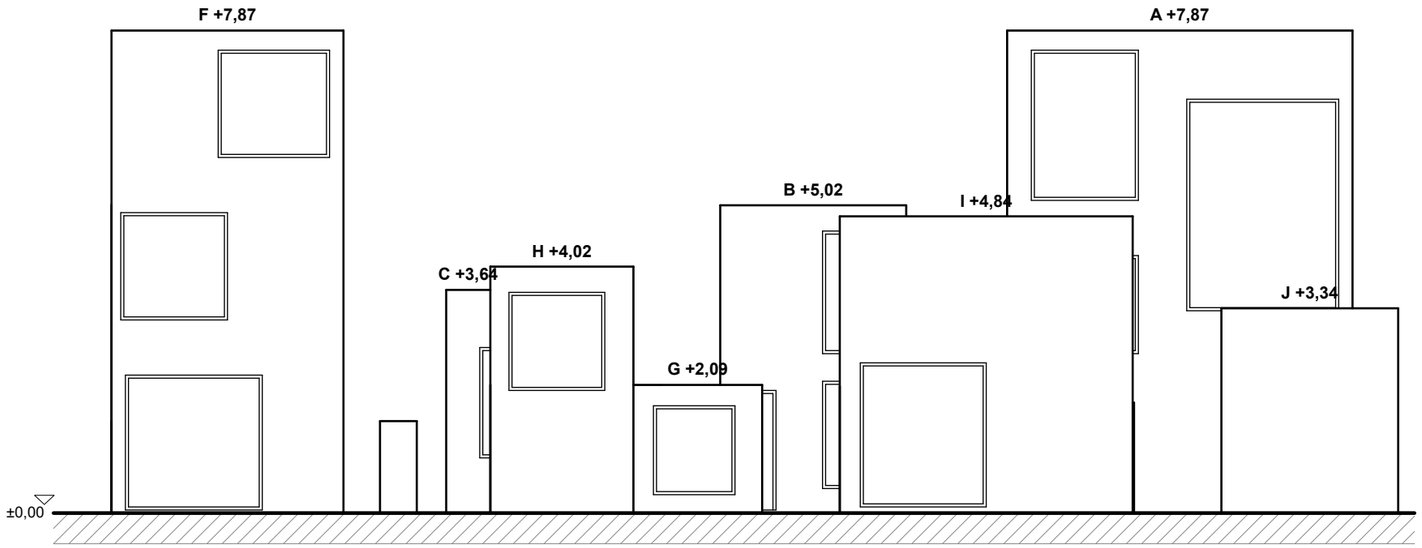

ALZADO SUR E 1:100

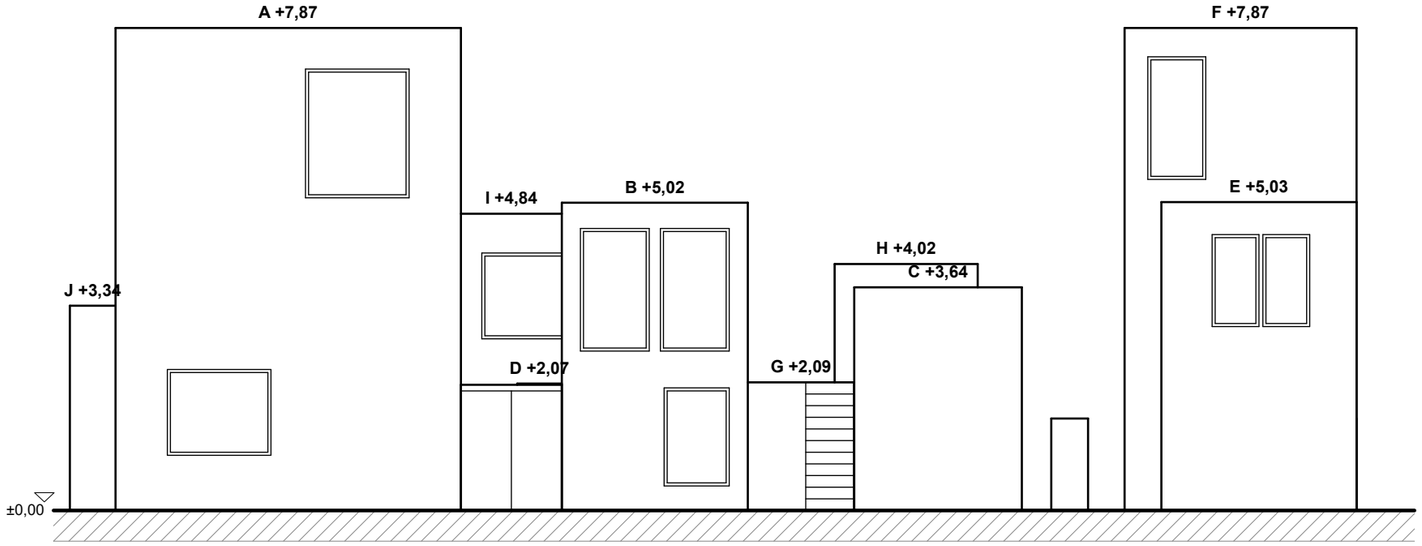


ALZADO NORTE E 1:100


CASA MORIYAMA

Ryue Nishizawa (SANAA) · Ota-ku, Tokio · 2002-2005 · Levantamiento

PLANO	ESCALA	
ALZADOS SUR Y NORTE	**1:100**	
PROYECTO BASE · H2 · Grupo X Fecha: octubre 2026 · Cotas en metros	Nº **05**	A3

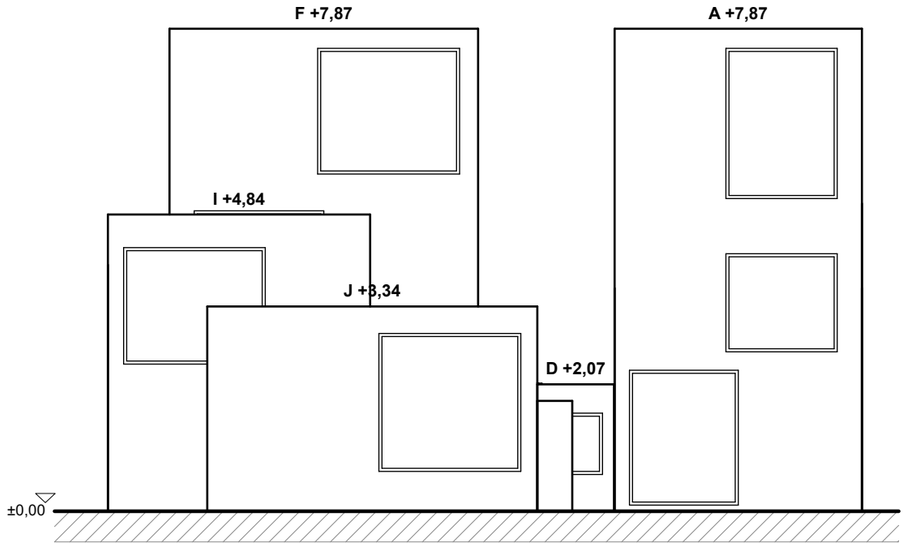

ALZADO ESTE E 1:100

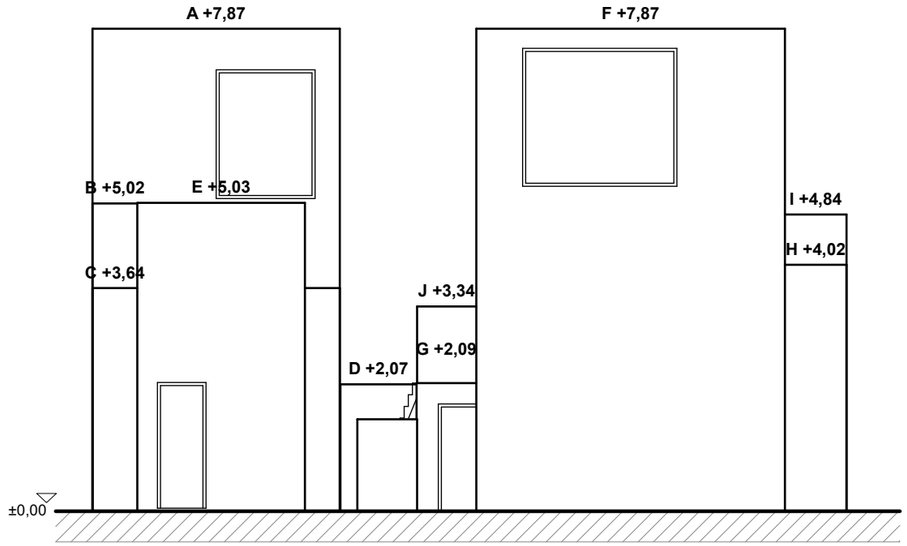


ALZADO OESTE E 1:100


CASA MORIYAMA

Ryue Nishizawa (SANAA) · Ota-ku, Tokio · 2002-2005 · Levantamiento

PLANO	ESCALA	
ALZADOS ESTE Y OESTE	**1:100**	
PROYECTO BASE · H2 · Grupo X Fecha: octubre 2026 · Cotas en metros	Nº **06**	A3

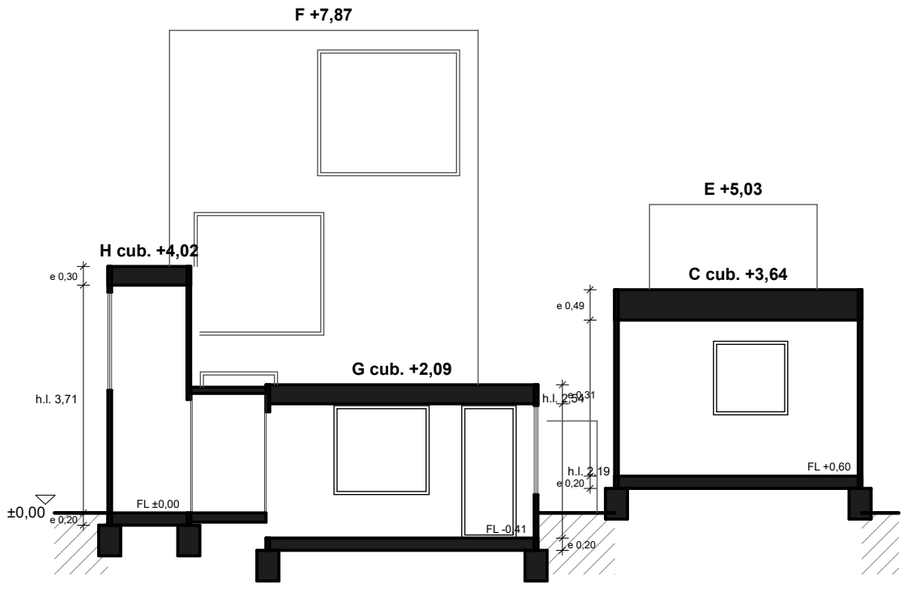

SECCIÓN A-A E 1:100

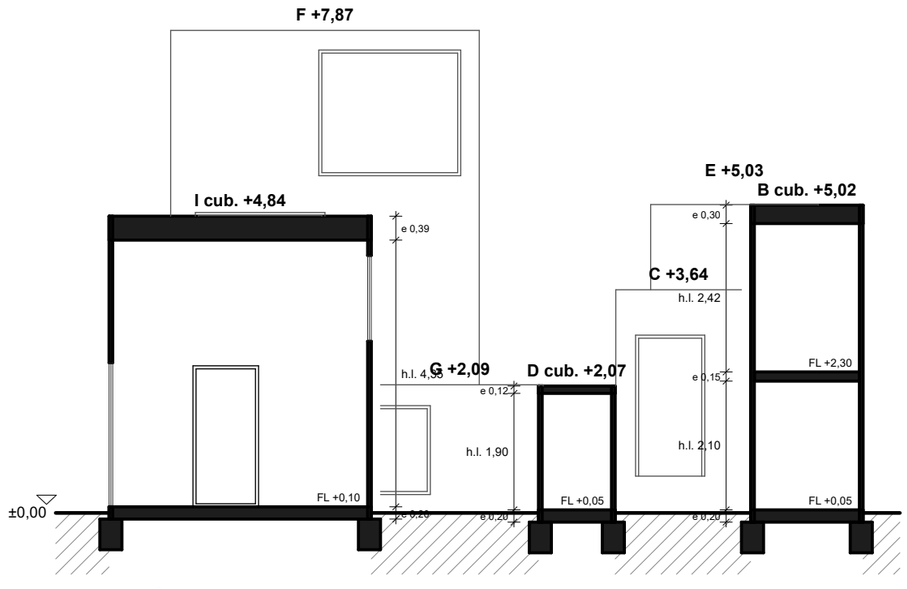


SECCIÓN B-B E 1:100

Muro: chapa de acero + aislamiento, e = 0,06 m
h.l. = altura libre · FL = nivel de suelo
Cotas en metros
e = espesor de forjado / cubierta
Forjados intermedios 0,15 (hipótesis) · solera 0,20


CASA MORIYAMA

Ryue Nishizawa (SANAA) · Ota-ku, Tokio · 2002-2005 · Levantamiento

PLANO	ESCALA	
SECCIONES A-A Y B-B	**1:100**	
PROYECTO BASE · H2 · Grupo X Fecha: octubre 2026 · Cotas en metros	Nº **07**	A3

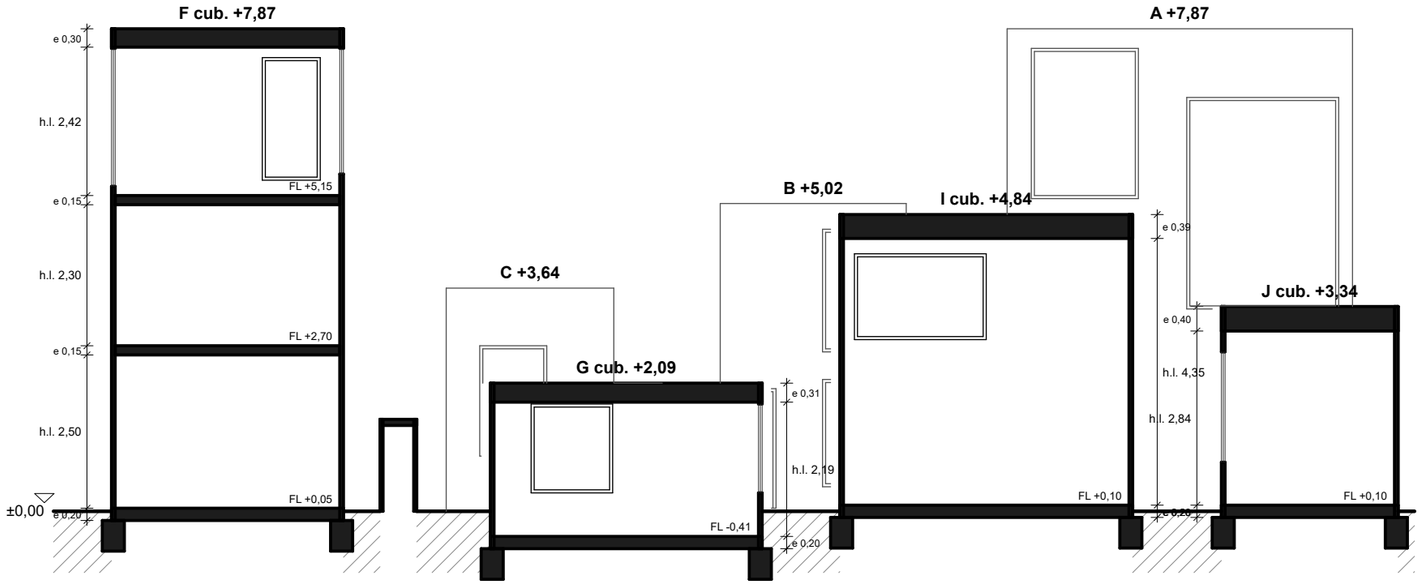

SECCIÓN C-C E 1:100

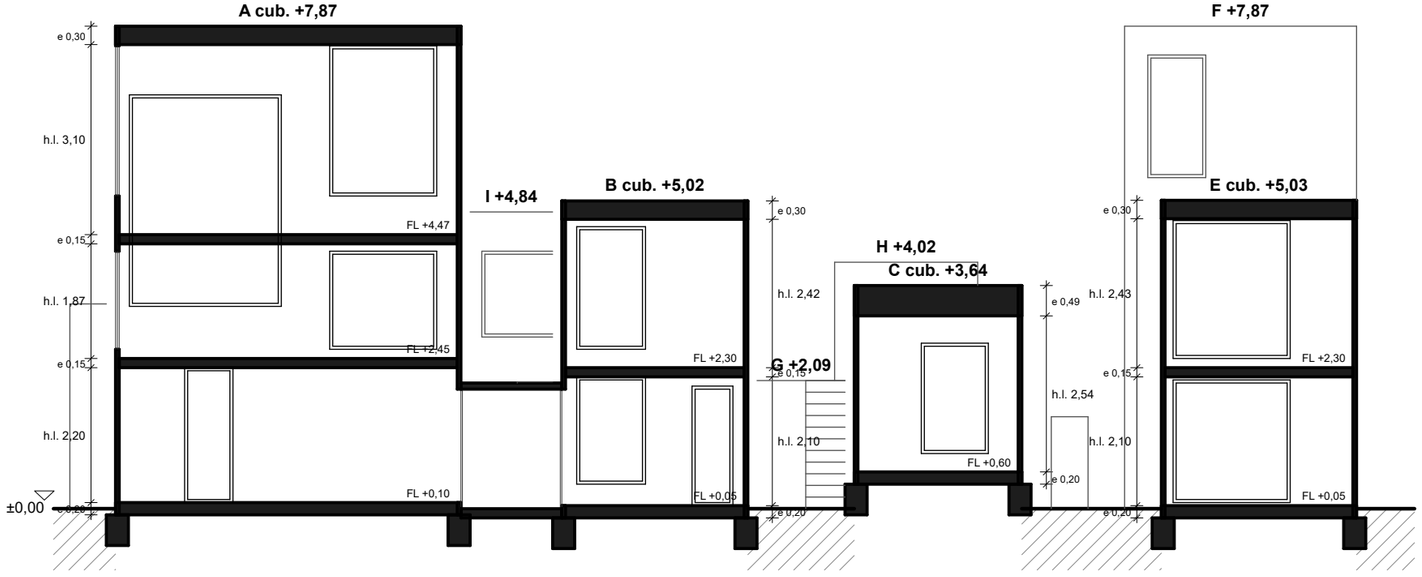

SECCIÓN D-D E 1:100

CASA MORIYAMA

Ryue Nishizawa (SANAA) · Ota-ku, Tokio · 2002-2005 · Levantamiento

PLANO	ESCALA	
SECCIONES C-C Y D-D	**1:100**	
PROYECTO BASE · H2 · Grupo X Fecha: octubre 2026 · Cotas en metros	Nº **08**	A3



SECCIÓN D-D (tramo cajas B y A)


E 1:50

Muro: chapa de acero + aislamiento, e = 0,06 m
h.l. = altura libre · FL = nivel de suelo
Cotas en metros
e = espesor de solera / forjado / cubierta
Forjados intermedios 0,15 (hipótesis) · solera 0,20
Mirando al sur

CASA MORIYAMA

Ryue Nishizawa (SANAA) · Ota-ku, Tokio · 2002-2005 · Levantamiento

PLANO	ESCALA	
SECCIÓN D-D · CAJAS B Y A	**1:50**	
PROYECTO BASE · H2 · Grupo X Fecha: octubre 2026 · Cotas en metros	Nº **09**	A3

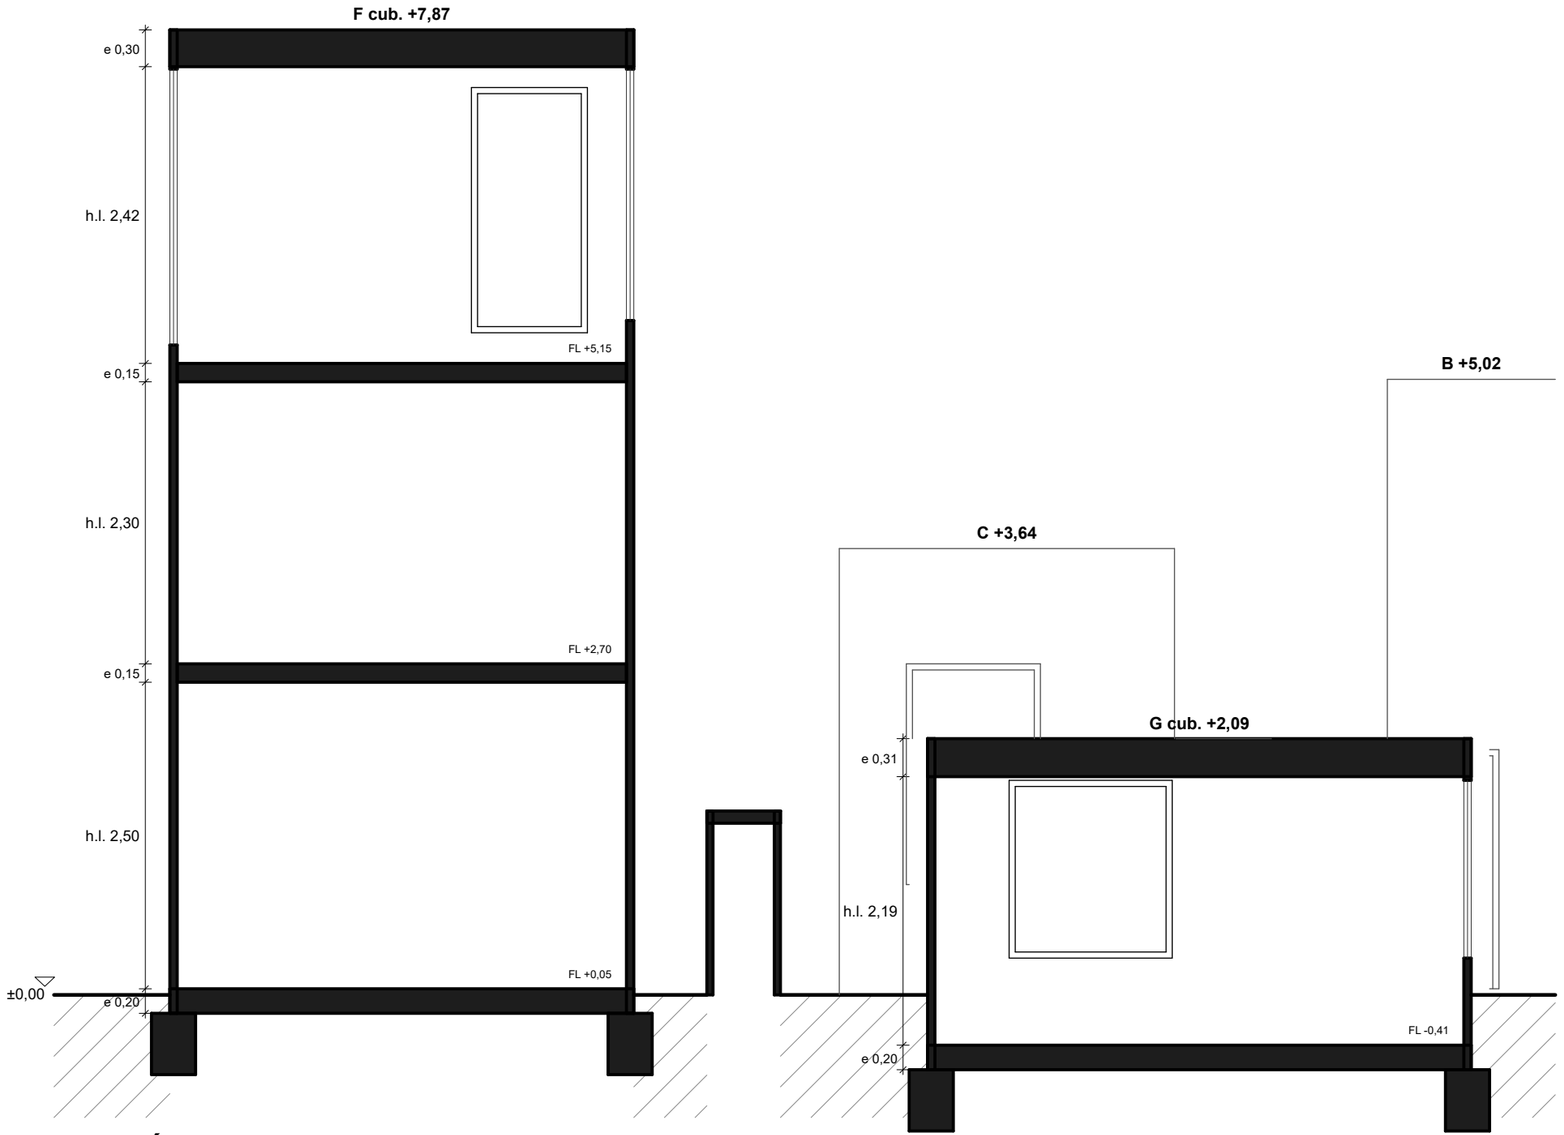

SECCIÓN C-C (tramo cajas F y G)


E 1:50

Muro: chapa de acero + aislamiento, e = 0,06 m
h.l. = altura libre · FL = nivel de suelo
Cotas en metros
e = espesor de solera / forjado / cubierta
Forjados intermedios 0,15 (hipótesis) · solera 0,20
Mirando al norte

CASA MORIYAMA


Ryue Nishizawa (SANAA) · Ota-ku, Tokio · 2002-2005 · Levantamiento

PLANO	ESCALA	
SECCIÓN C-C · CAJAS F Y G	**1:50**	
PROYECTO BASE · H2 · Grupo X Fecha: octubre 2026 · Cotas en metros	Nº **10**	A3

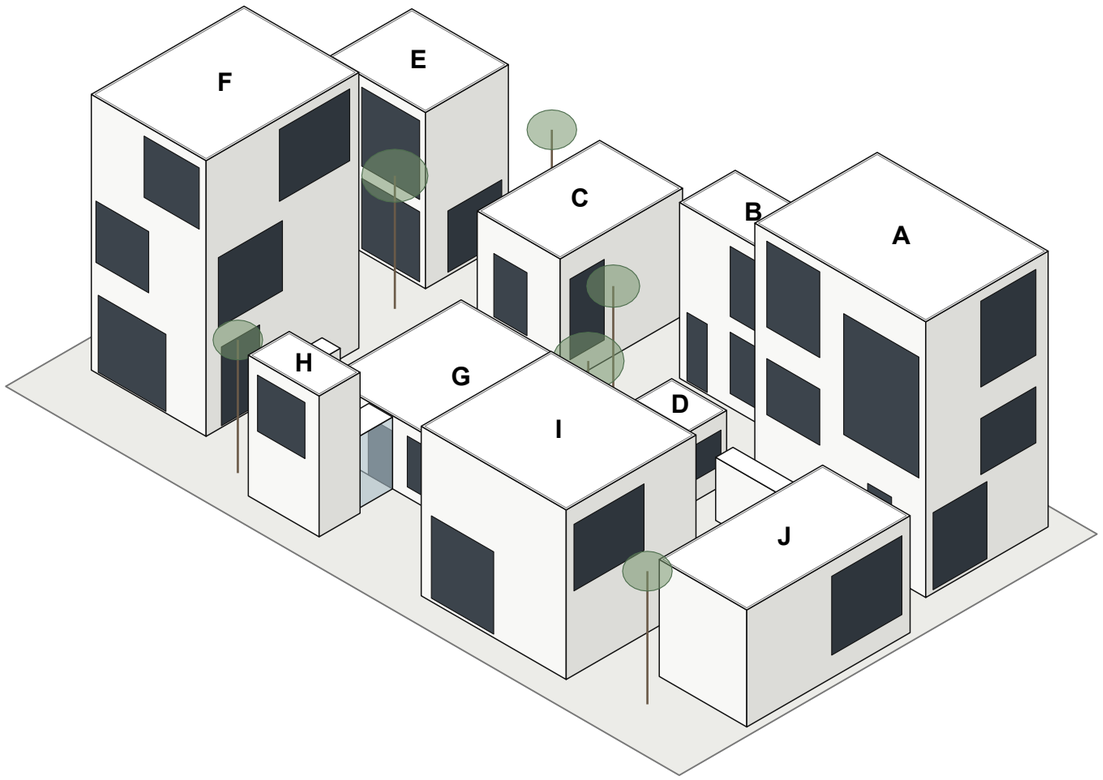

VISTA DESDE EL SURESTE

Volumetría generada a partir de las cotas del levantamiento. Huecos de vidrio en gris oscuro.

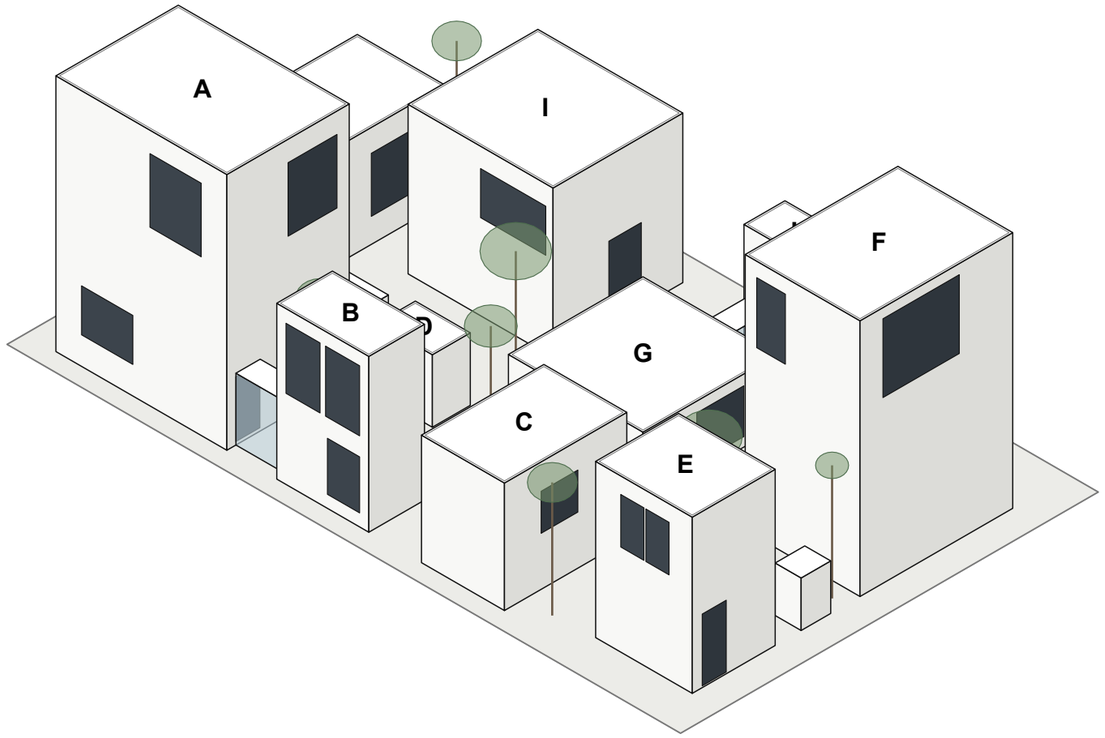

VISTA DESDE EL NOROESTE

CASA MORIYAMA

Ryue Nishizawa (SANAA) · Ota-ku, Tokio · 2002-2005 · Levantamiento

PLANO	ESCALA	
AXONOMETRÍAS	**S/E**	
PROYECTO BASE · H2 · Grupo X Fecha: octubre 2026 · Cotas en metros	Nº **11**	A3

IMÁGENES DEL PROYECTO

Renders realizados con el motor de renderizado de Revit 2026 sobre el modelo BIM (CasaMoriyama.rvt)



Vista desde la calle este




Calle sur: cajas H, G e I



Paso entre cajas



Vista aérea desde el sureste

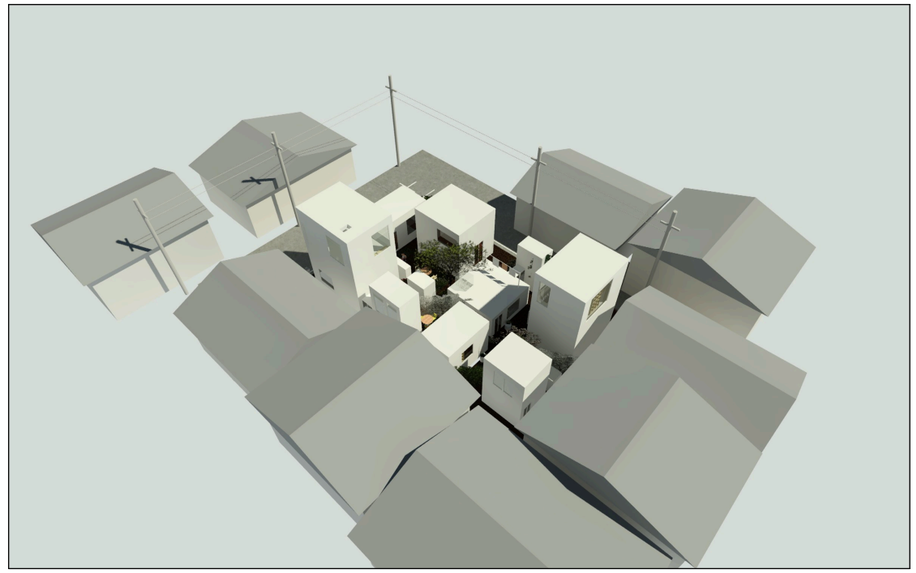

Vista aérea desde el noroeste

CASA MORIYAMA

Ryue Nishizawa (SANAA) · Ota-ku, Tokio · 2002-2005 · Levantamiento

PLANO	ESCALA	
IMÁGENES (RENDERS REVIT)	**S/E**	
PROYECTO BASE · H2 · Grupo X Fecha: octubre 2026 · Cotas en metros	Nº **12**	A3