PROYECTO BASE · H2 · GRUPO X

Casa Moriyama

Ryue Nishizawa (SANAA)

Ota-ku, Tokio · 2002–2005

Levantamiento gráfico: plantas, secciones, alzados y volumetría



LA OBRA

Una casa partida en diez

10
cajas independientes (A–J)

290 m²
de parcela

263 m²
construidos

6 cm
de espesor de muro


1–3
plantas por caja

7,87 m
caja más alta (A y F)

Encargo de Yasuo Moriyama en un barrio residencial de Tokio. En lugar de un edificio, Nishizawa reparte el programa en volúmenes blancos de acero separados por pequeños jardines: cada estancia, incluso el baño, es un edificio.

Deshacer la casa

- **Vivienda del propietario** en las cajas A, B, C, D: salón, cocina, estudio y baño separados.
- **Cinco apartamentos de alquiler** (E, F, G+H, I, J). El propietario decide cuánto ocupa y cuánto alquila.
- Los **jardines entre cajas** son parte de la casa: para ir del salón al baño se sale al exterior.
- Sin vallas: la calle, los vecinos y los patios se entrelazan.

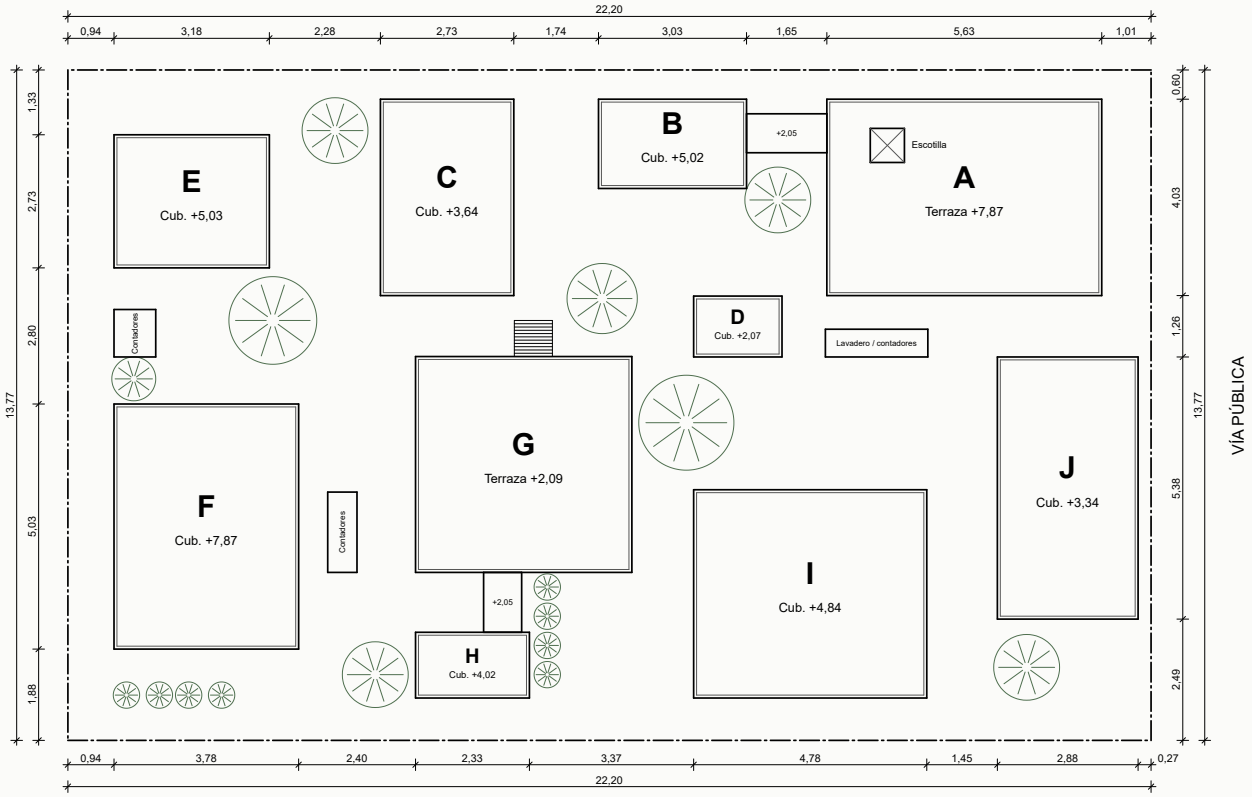


PROGRAMA


Las diez cajas

CAJA	USO POR PLANTA	PLANTA (M)	PL.	ALTURA LIBRE (M)	CUBIERTA	
A	Salón / Estudio / almacén (techo bajo) / Dormitorio-estudio	5,63 × 4,03	3	2,20 · 1,87 · 3,10	+7,87	Propietario
B	Cocina-comedor / Dormitorio	3,03 × 1,83	2	2,10 · 2,42	+5,02	Propietario
C	Estudio-salón	2,73 × 4,03	1	2,54	+3,64	Propietario
D	Baño	1,81 × 1,25	1	1,90	+2,07	Propietario
E	Cocina-comedor / Dormitorio	3,18 × 2,73	2	2,10 · 2,43	+5,03	Alquiler
F	Salón-comedor-cocina / Dormitorio + baño / Estudio	3,78 × 5,03	3	2,50 · 2,30 · 2,42	+7,87	Alquiler
G	Salón (semisótano)	4,43 × 4,43	1	2,19	+2,09	Alquiler
H	Baño (de G)	2,33 × 1,35	1	3,71	+4,02	Alquiler
I	Salón-dormitorio	4,78 × 4,28	1	4,35	+4,84	Alquiler
J	Salón-dormitorio + baño	2,88 × 5,38	1	2,84	+3,34	Alquiler


Distribución acotada · E 1:100

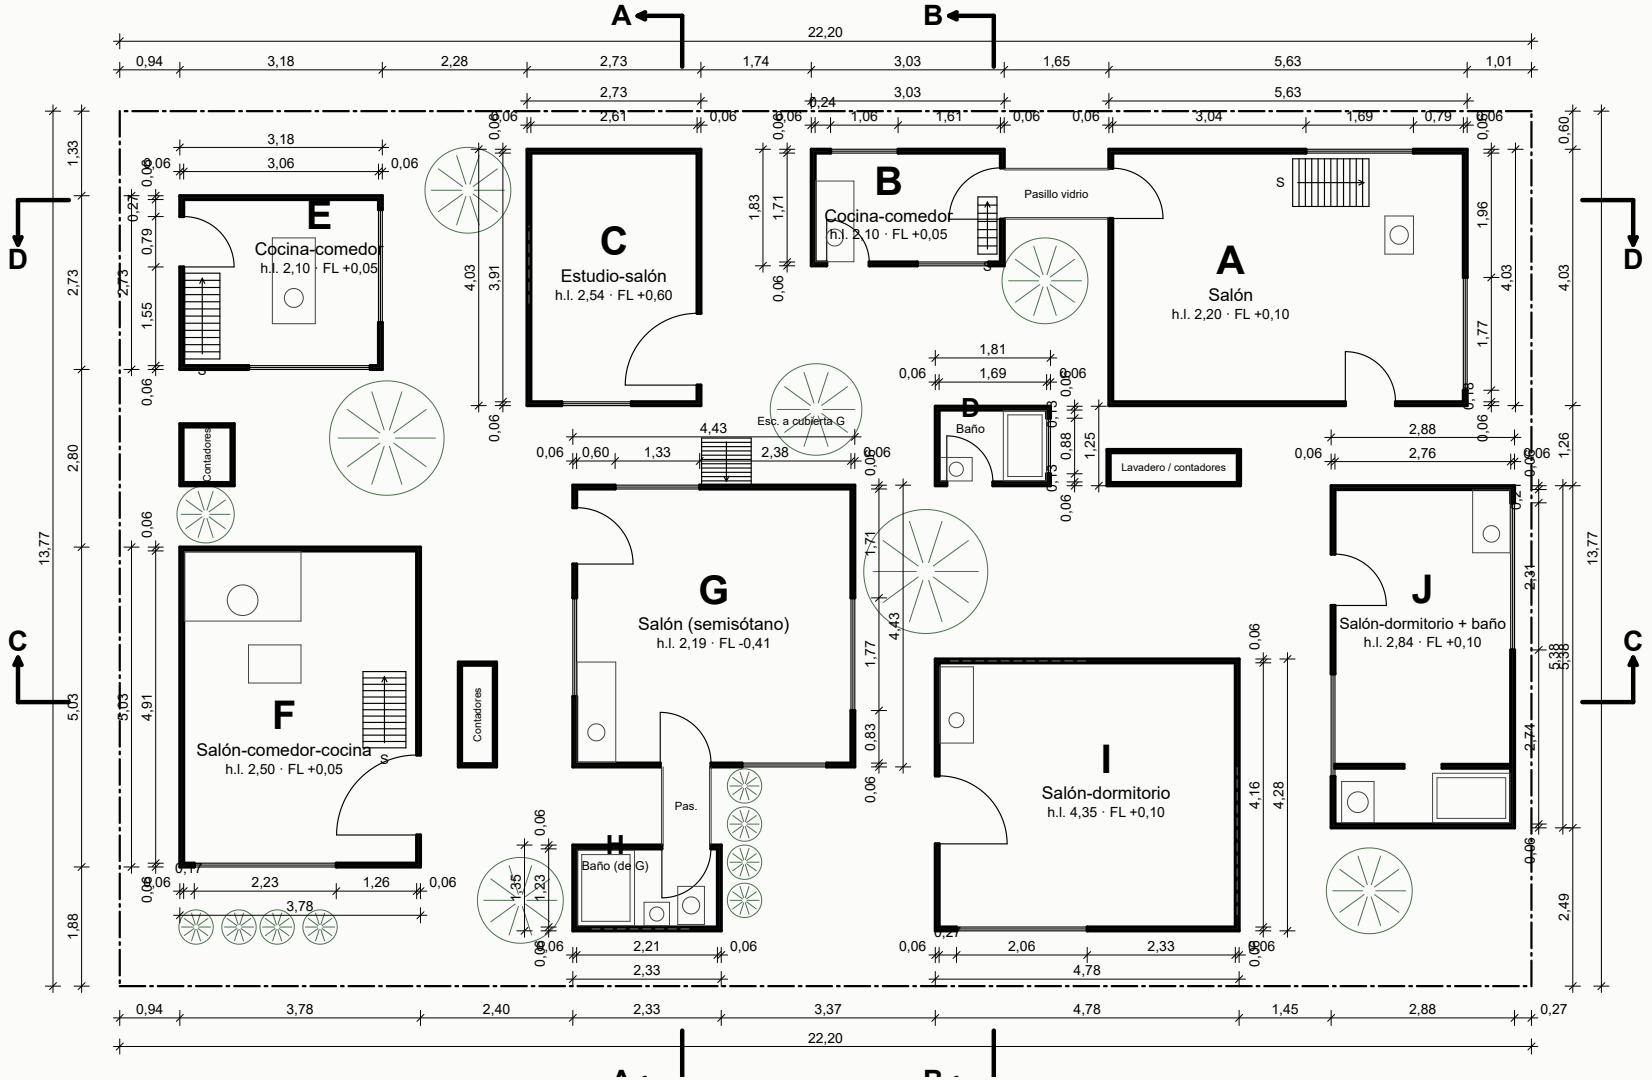

Planta primera y planta segunda

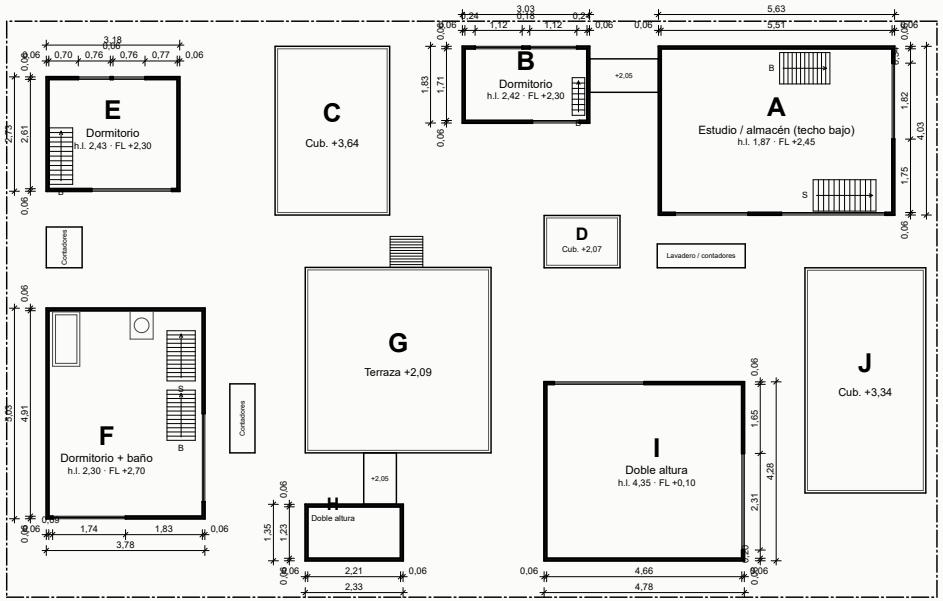


Planta primera (+3,80): A, B, E, F; I y H en doble altura

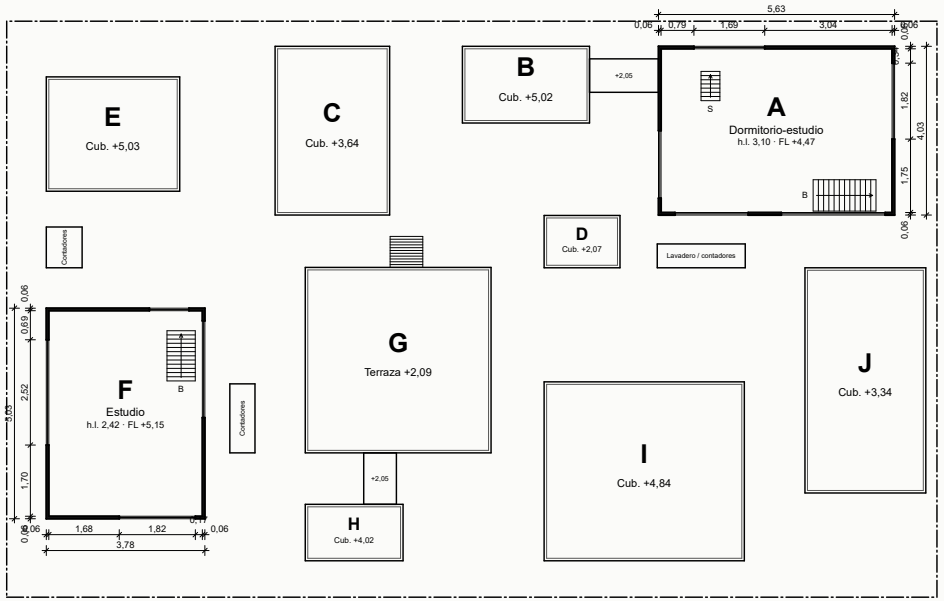

Planta segunda (+6,20): solo A y F

Cajas B y A


- **A**: tres plantas con alturas libres de 2,20 · 1,87 · 3,10 m. La planta intermedia es un estudio-almacén de techo bajo.
- Forjados de 0,15 m, solera de 0,20 m y cubierta de 0,30 m. **Cota de cubierta +7,87** (terraza con escotilla).
- **B**: dos plantas, con 2,10 y 2,42 m de altura libre. Cubierta a +5,02.
- Pasillo de vidrio entre B y A (h.l. 1,85).

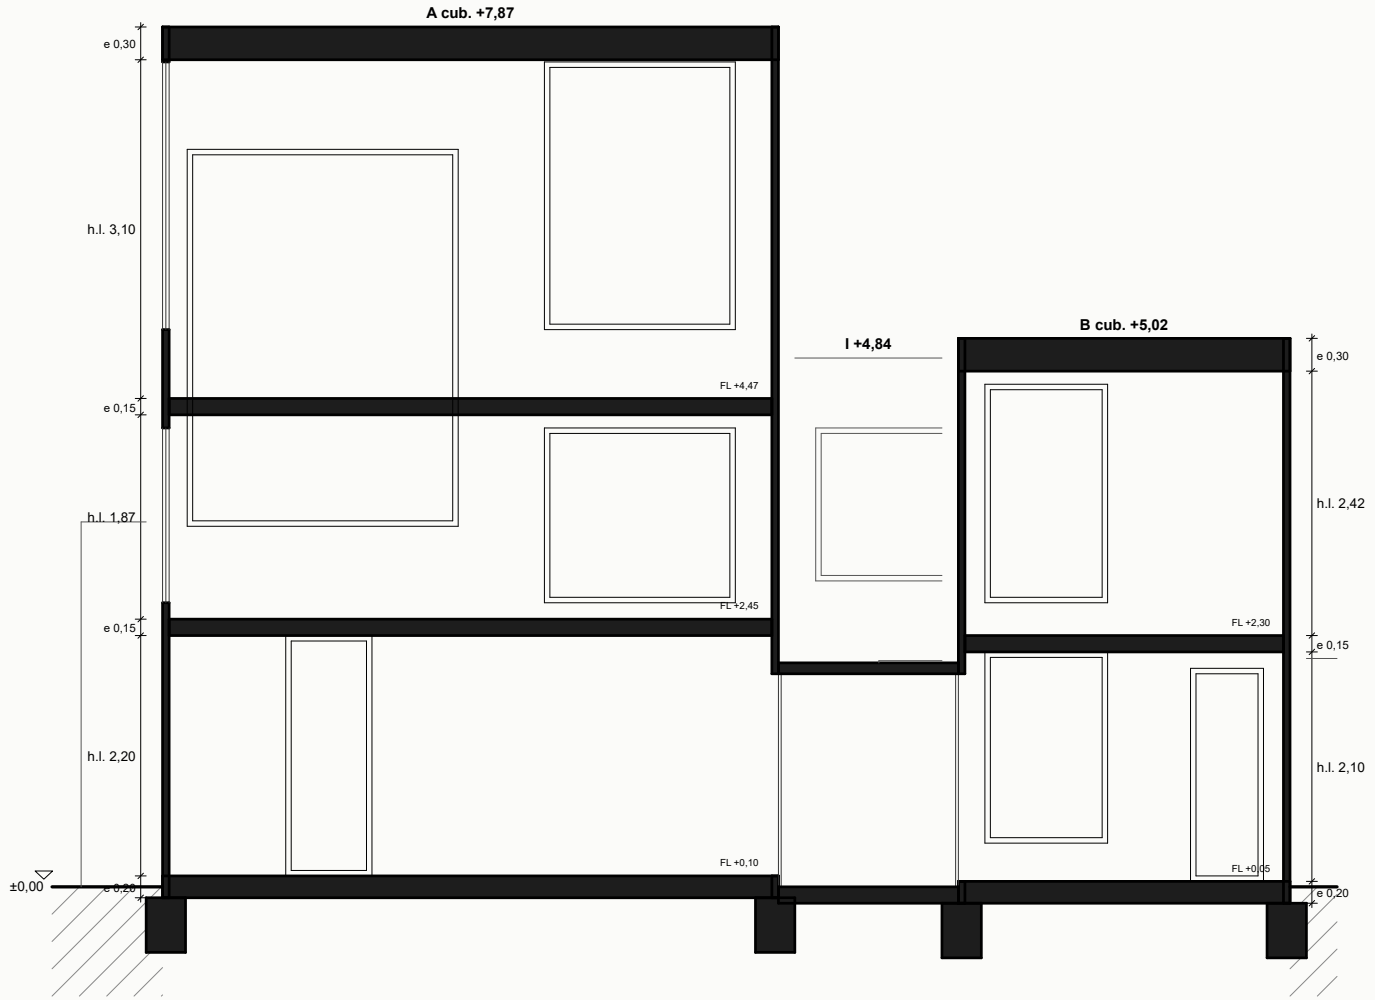

SECCIÓN D-D (tramo cajas B y A) E 1:50


Cajas F y G

- **F**: tres plantas (2,50 · 2,30 · 2,42 m). Cubierta a +7,87, la misma altura que A, fijada por el límite de altura.
- **G**: salón en semisótano (suelo a −0,41) con 2,19 m de altura libre.
- La cubierta de G (+2,09) es una terraza a la que se sube por una escalera exterior.

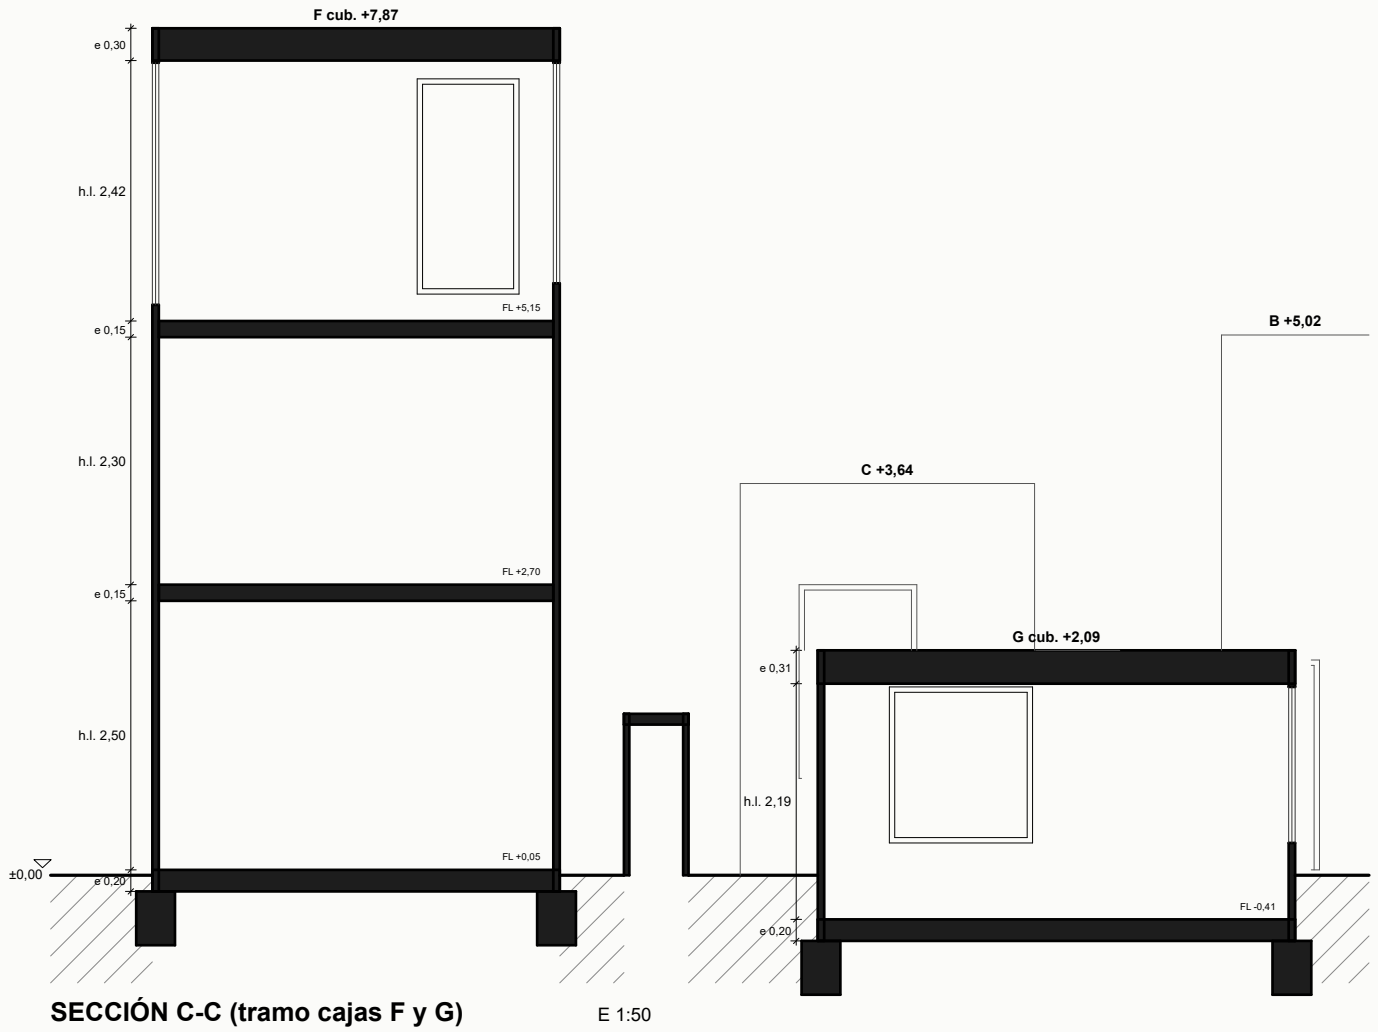


SECCIÓN C-C (tramo cajas F y G) E 1:50

Sur y norte · E 1:100

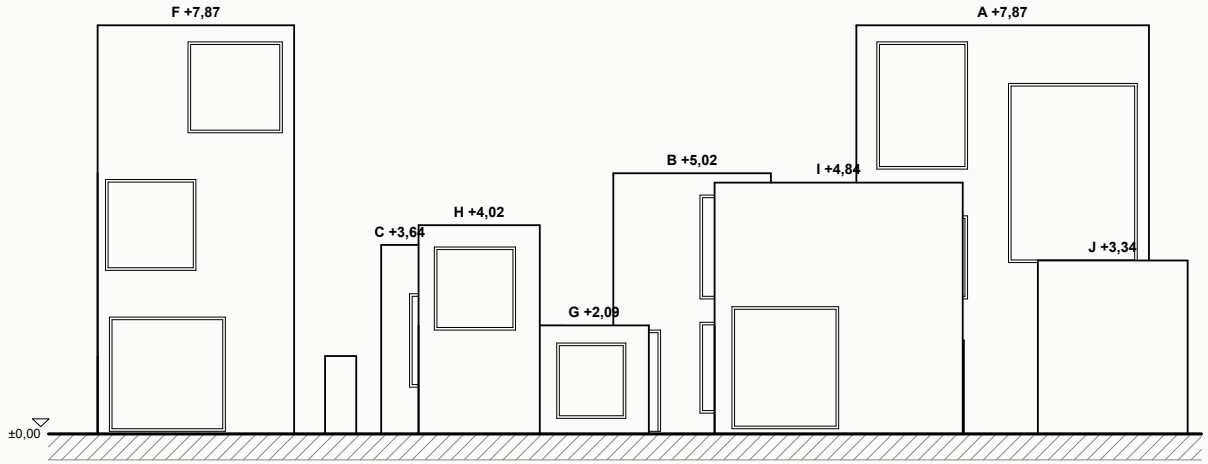


ALZADO SUR E 1:100

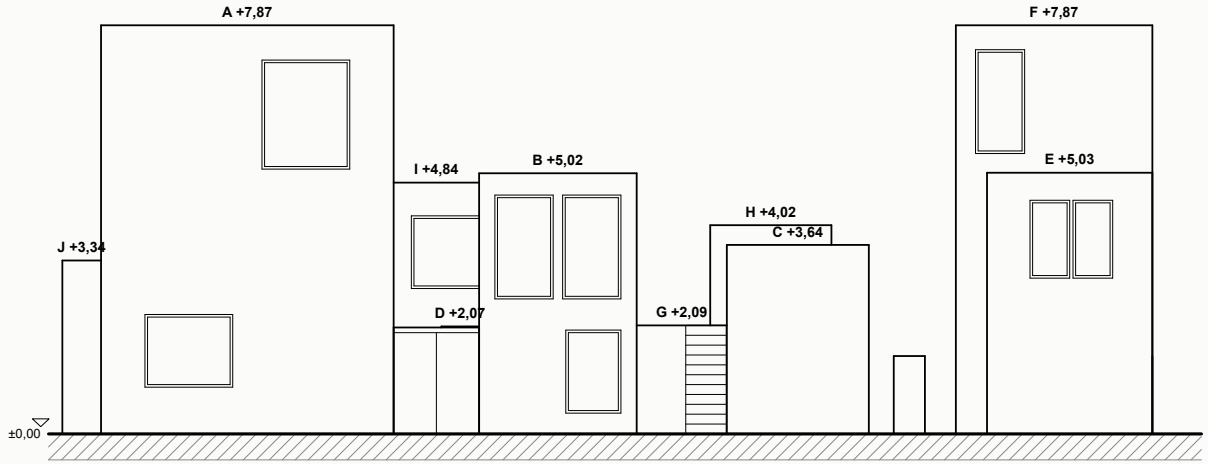


ALZADO NORTE E 1:100

Axonometrías

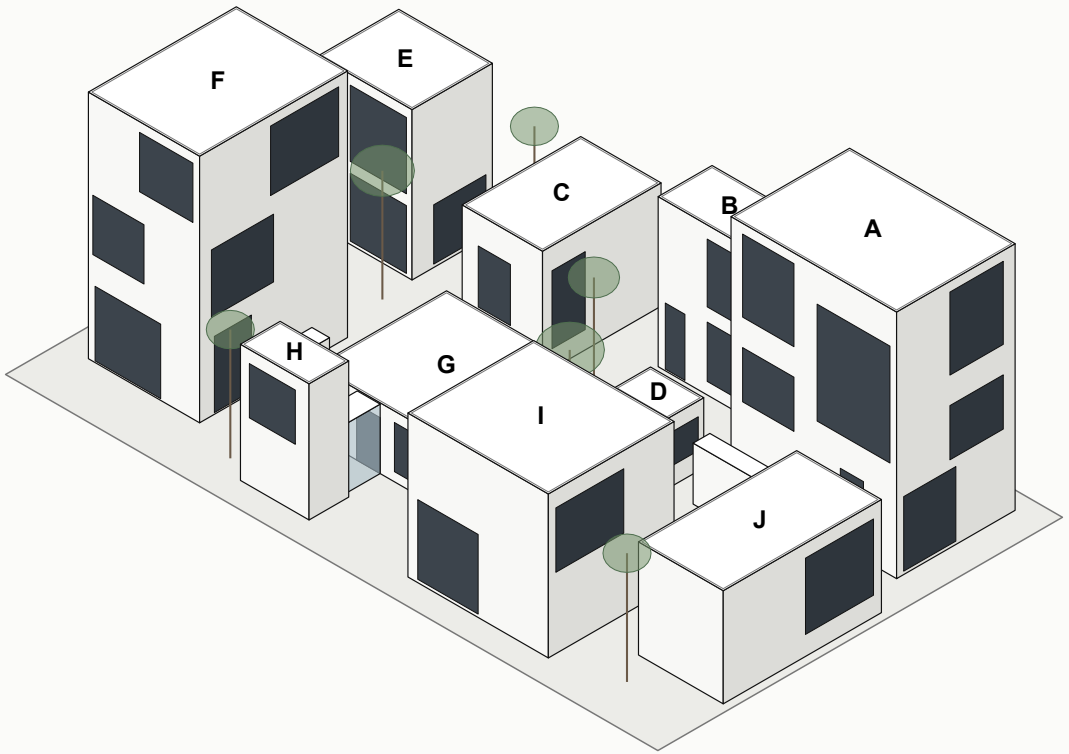

Desde el sureste

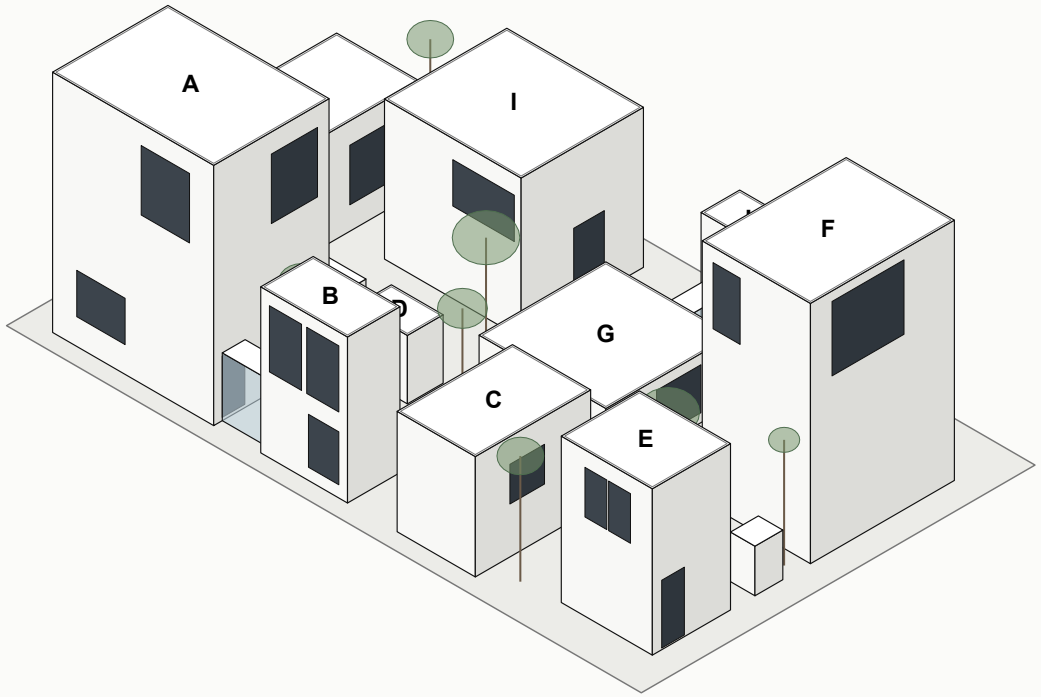


Desde el noroeste

MODELO BIM

Revit 2026

- El modelo se ha generado desde la misma base de datos que los planos: **56 muros** de chapa de 6 cm, **32 losas** y **52 huecos** con vidrio y marco.
- **111 elementos** de mobiliario, sanitarios, vegetación RPC y personas, colocados según la planta original.
- Materiales con apariencia de render, entorno de vecinos, postes y calles.
- Imágenes renderizadas con el **motor de render de Revit**.

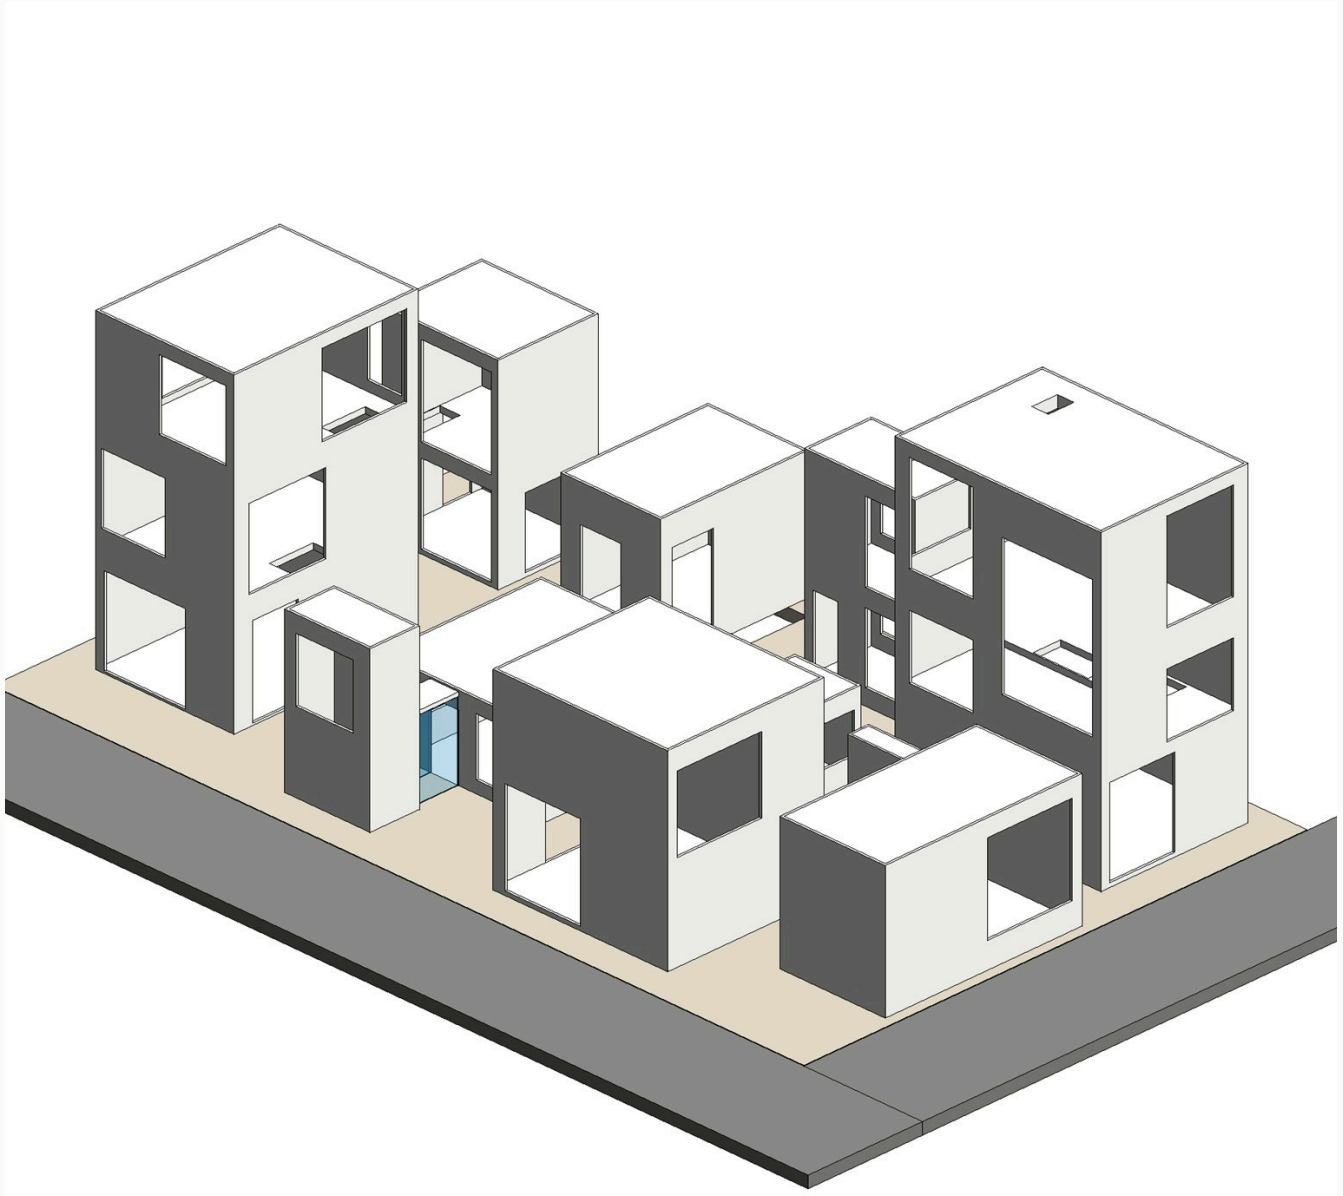



IMÁGENES · REVIT

Desde la calle

Las cajas blancas aparecen entre la vegetación, sin vallas, abiertas al barrio.

IMÁGENES · REVIT

Vivir entre cajas

IMÁGENES · REVIT

La casa en el barrio



IMÁGENES · REVIT

La terraza de G

La cubierta de una caja se convierte en el patio de otra.

Cajas de chapa de acero

Muros portantes


Chapa de acero estructural con aislamiento y acabado interior: 6 cm en total. No hay pilares ni vigas; la propia caja es la estructura.

Huecos


Grandes ventanas recortadas en la chapa, con la carpintería oculta. Su posición responde a las vistas entre cajas y a la privacidad frente a los vecinos.

Cubiertas y suelos

Cubiertas planas; las de A y G son terrazas transitables. Las cotas de suelo varían de −0,41 (G) a +0,60 (C).

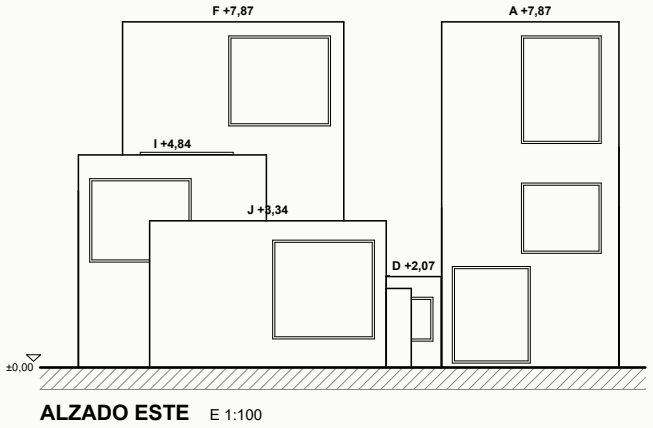

Alzado este · E 1:100

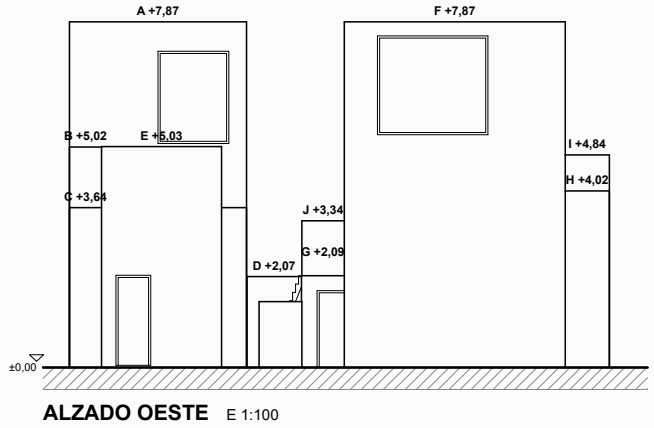

Alzado oeste · E 1:100

MÉTODO

Cómo se ha hecho el levantamiento

1. **Planta original** de la oficina de Nishizawa: cota de cada caja entre ejes (p. ej. A = 5,63 × 4,03 m).
2. **Secciones constructivas originales** (B-D-I y C-G-H) y **axonometría**, medidas a escala, para las alturas (±0,10–0,20 m).
3. **Maqueta 1:50 del MoMA** para los huecos de las fachadas norte y oeste.
4. Todos los datos en una **base única** (moriyama.json), de la que salen los planos en DWG y PDF y el **modelo BIM en Revit 2026** con sus renders.

Hipótesis señaladas en los planos: forjados intermedios de 0,15 y algunos huecos de las fachadas norte y oeste.

Gracias

¿Preguntas?

