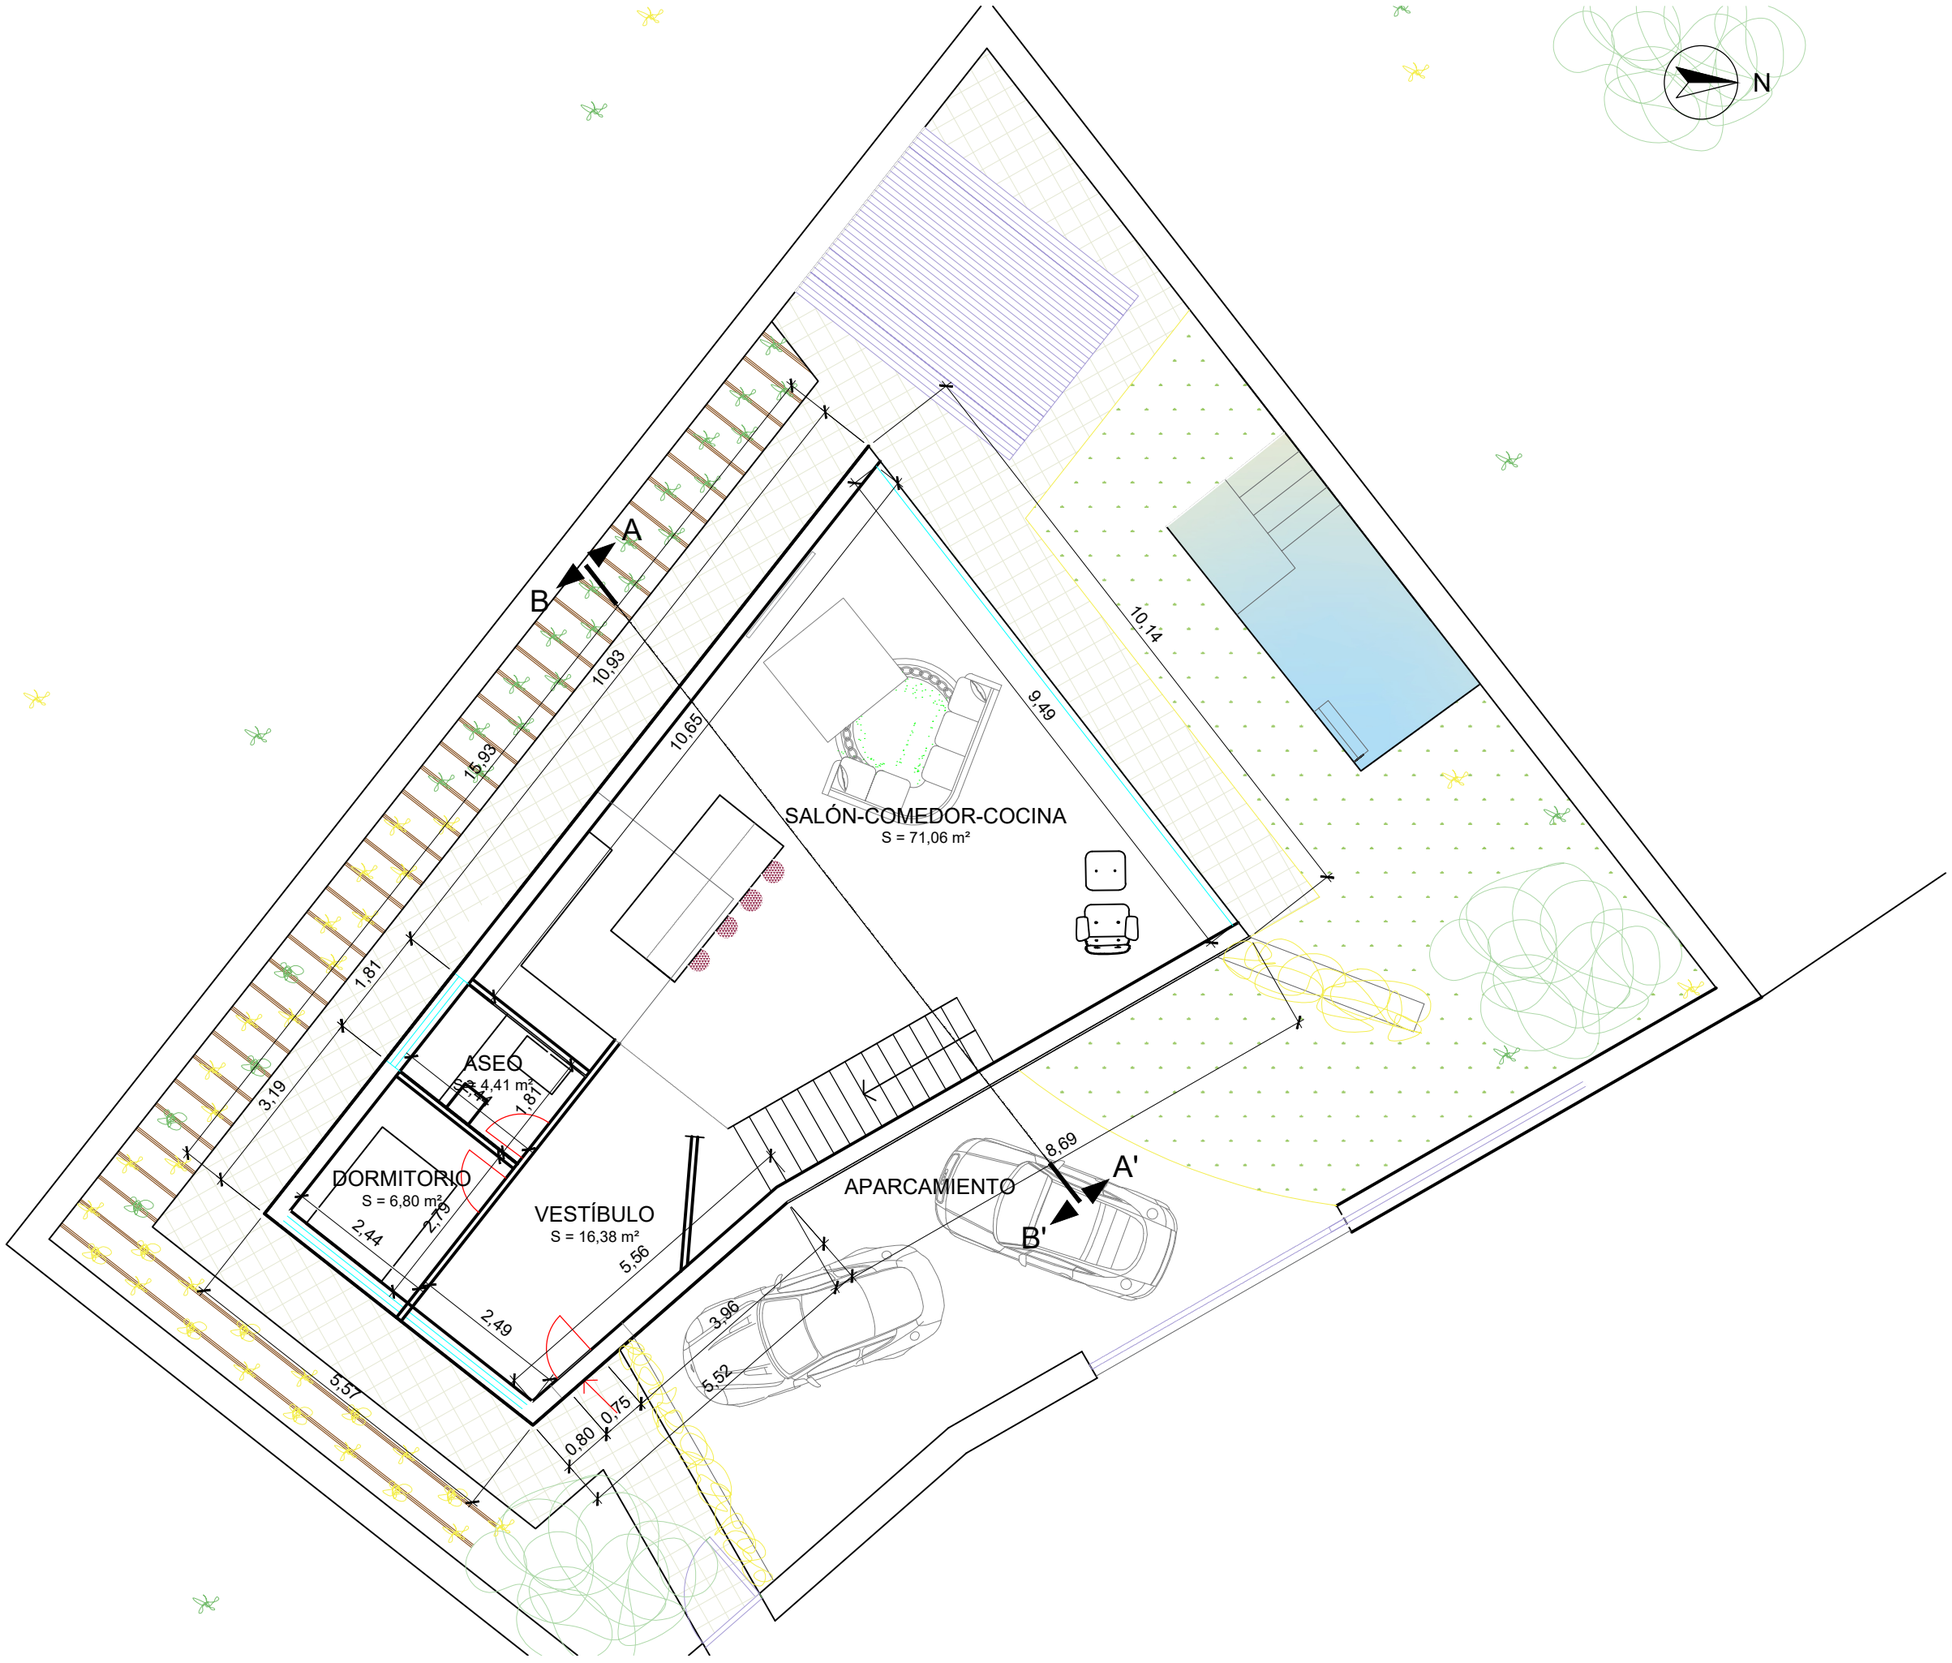


CUADRO DE SUPERFICIES

PLANTA BAJA	
Dormitorio	6,80 m²
Aseo	4,41 m²
Vestíbulo	16,38 m²
Salón-comedor-cocina	71,06 m²
Total útil planta baja	98,65 m²
PLANTA PRIMERA	
Dormitorio principal	25,09 m²
Baño	8,61 m²
Distribuidor	3,81 m²
Total útil planta primera	37,50 m²
TOTAL SUPERFICIE ÚTIL	136,15 m²
Construida planta baja	111,18 m²
Construida planta primera	44,77 m²
TOTAL SUPERFICIE CONSTRUIDA	155,95 m²

PLANTA BAJA
E 1:100

PLANTA BAJA
PROYECTO DE VIVIENDA UNIFAMILIAR
DANIEL
C.F.G.S. PROYECTOS DE EDIFICACIÓN
MÓDULO: REPRESENTACIONES DE CONSTRUCCIÓN

ESCALA: 1:100
FECHA 26 OCT 26
ALUMNO Fdo: Alejandro Gómez Jiménez
PLANO Nº 2



PLANTA PRIMERA

E 1:100

LE REBECO

PLANTA PRIMERA

PROYECTO DE VIVIENDA UNIFAMILIAR

DANIEL

C.F.G.S. PROYECTOS DE EDIFICACIÓN

MÓDULO: REPRESENTACIONES DE CONSTRUCCIÓN

ESCALA: 1:100


FECHA 26 OCT 26

ALUMNO Fdo: Alejandro Gómez Jiménez

PLANO Nº 3




PLANTA DE CUBIERTA
E 1:100

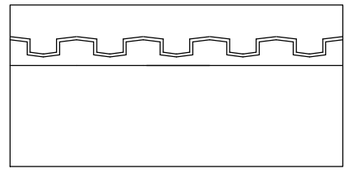

DETALLE DE CAPAS DE CUBIERTA (S/E)
SIN ESCALA


PLANTA DE CUBIERTA
PROYECTO DE VIVIENDA UNIFAMILIAR
DANIEL
C.F.G.S. PROYECTOS DE EDIFICACIÓN
MÓDULO: REPRESENTACIONES DE CONSTRUCCIÓN

ESCALA: INDICADAS
FECHA 26 OCT 26
ALUMNO Fdo: Alejandro Gómez Jiménez
PLANO Nº 4

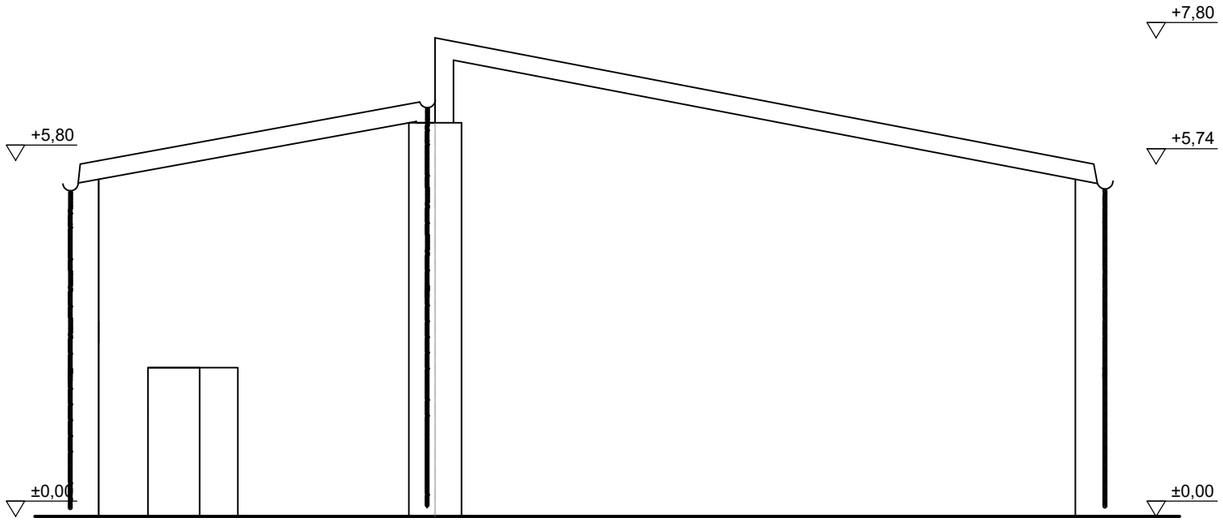


ALZADO B

E 1:100

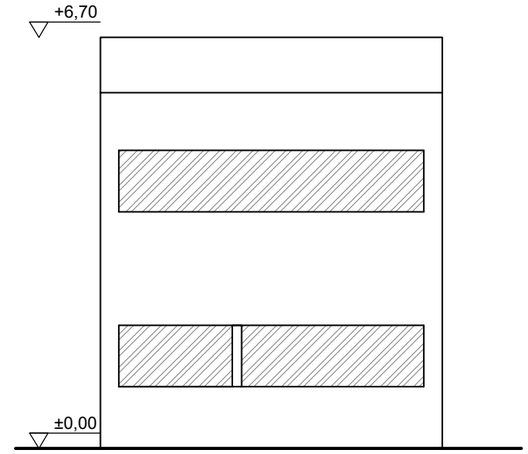


ALZADO A

E 1:100

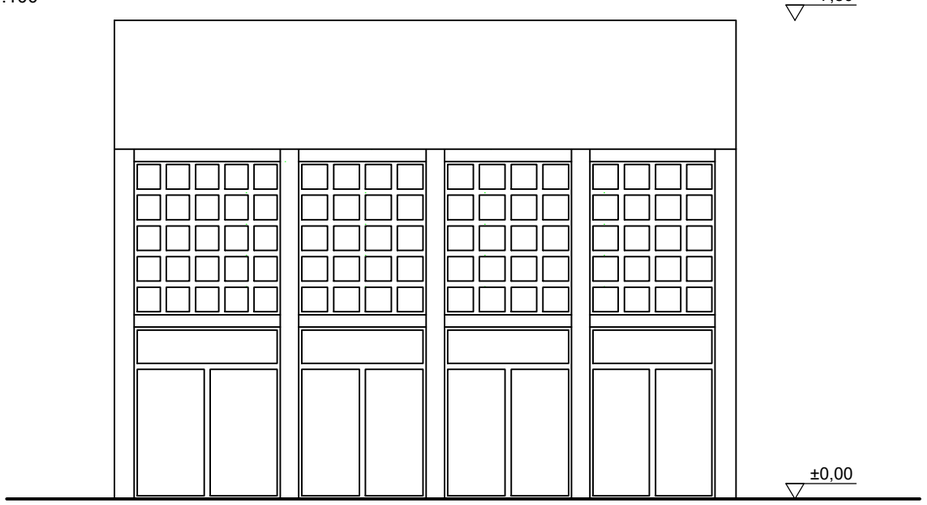

ALZADO C

E 1:100

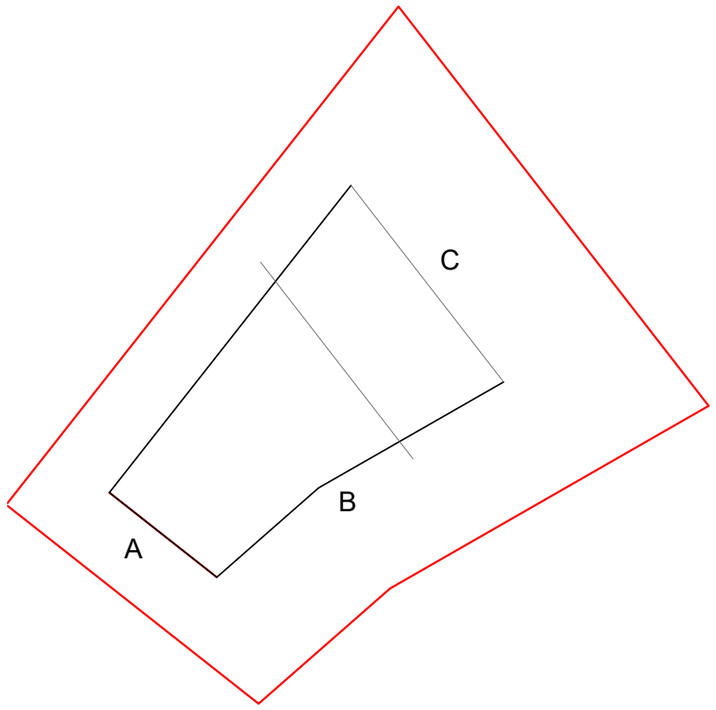

PLANO GUÍA

E 1:250

ALZADOS

PROYECTO DE VIVIENDA UNIFAMILIAR

DANIEL

C.F.G.S. PROYECTOS DE EDIFICACIÓN


MÓDULO: REPRESENTACIONES DE CONSTRUCCIÓN


ESCALA: INDICADAS

FECHA 26 OCT 26

ALUMNO Fdo: Alejandro Gómez Jiménez

PLANO Nº 5

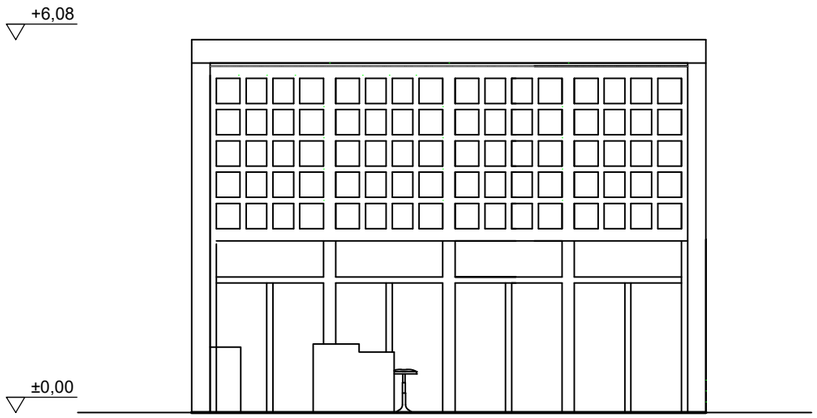


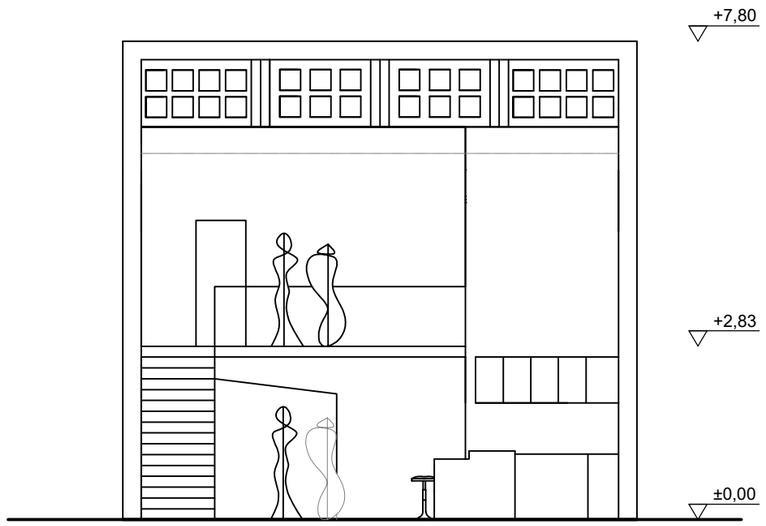

Sección A-A' Sección B-B'

SECCIONES A-A' Y B-B'

E 1:100

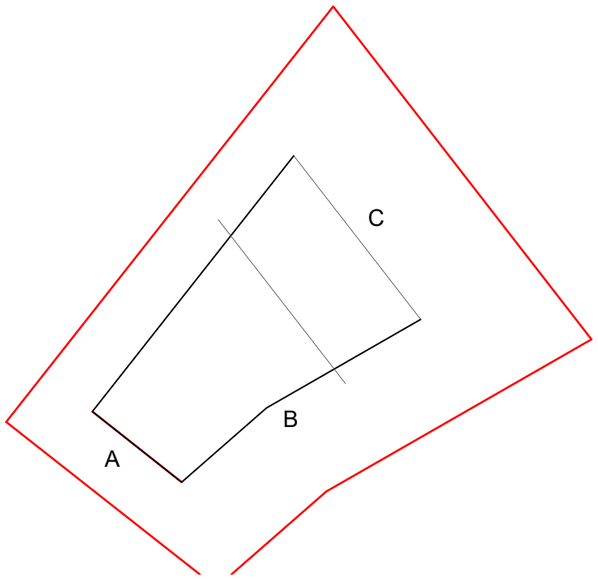

PLANO GUÍA

E 1:300

SECCIONES

PROYECTO DE VIVIENDA UNIFAMILIAR

DANIEL

C.F.G.S. PROYECTOS DE EDIFICACIÓN


MÓDULO: REPRESENTACIONES DE CONSTRUCCIÓN

ESCALA: INDICADAS

FECHA 26 OCT 26


ALUMNO Fdo: Alejandro Gómez Jiménez

PLANO Nº 6

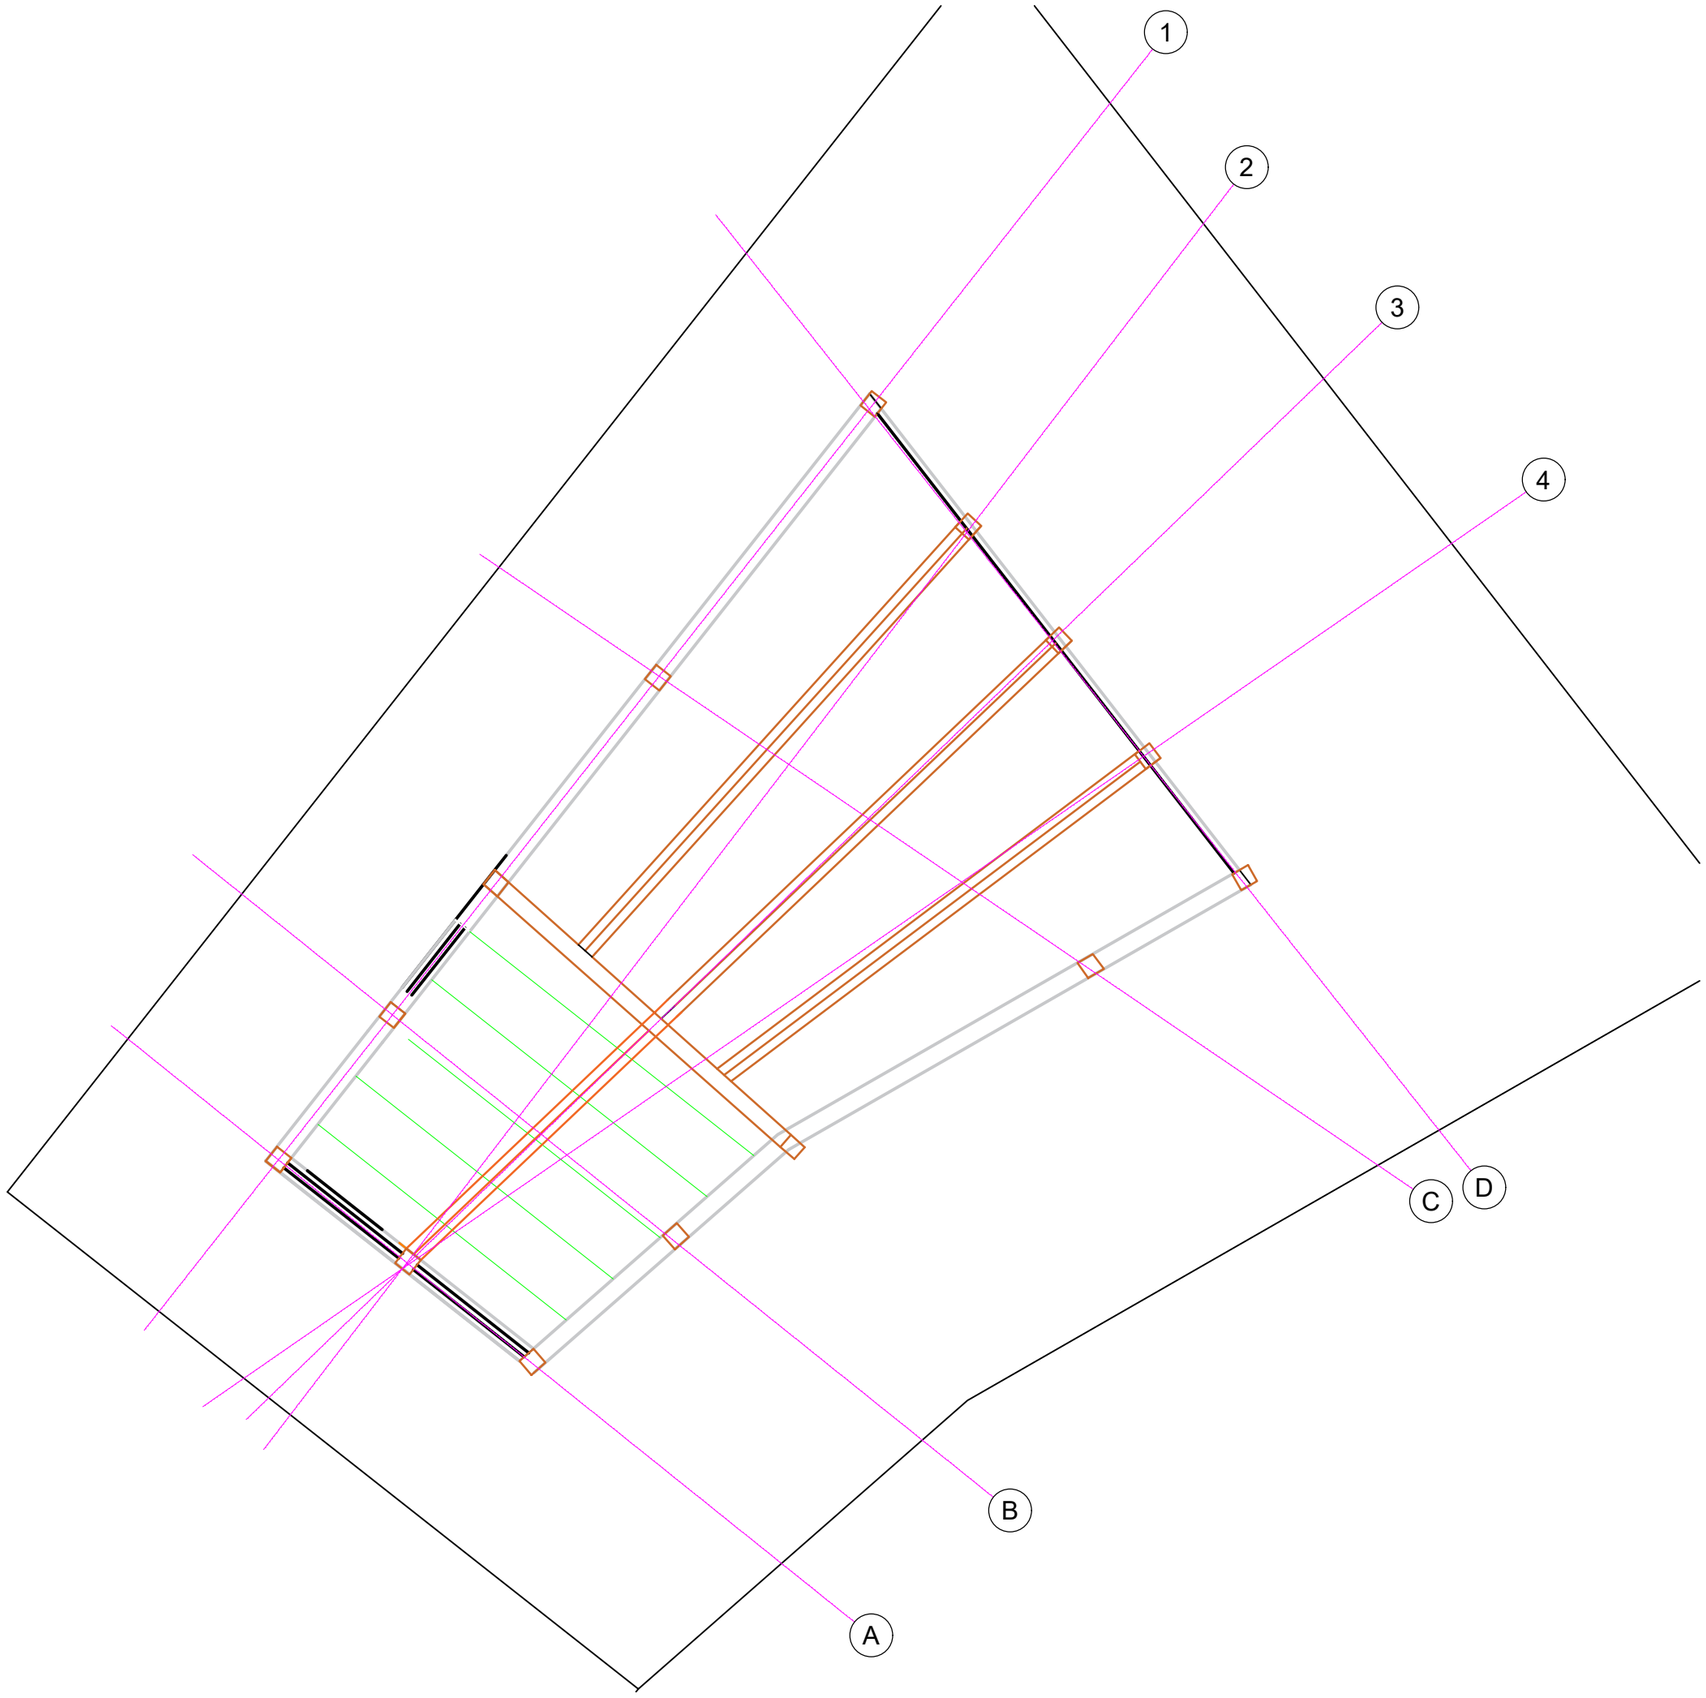


ESTRUCTURA Y EJES DE REPLANTEO

E 1:100

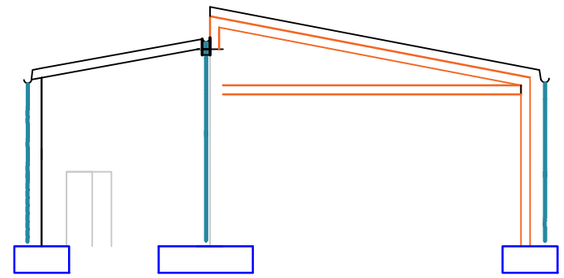

PÓRTICO TIPO (S/E)

SIN ESCALA

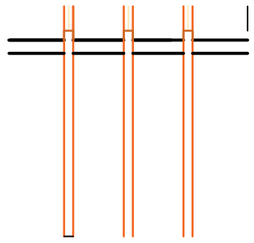

PÓRTICO LONGITUDINAL (S/E)

SIN ESCALA

ESTRUCTURA Y EJES

PROYECTO DE VIVIENDA UNIFAMILIAR

DANIEL

C.F.G.S. PROYECTOS DE EDIFICACIÓN

MÓDULO: REPRESENTACIONES DE CONSTRUCCIÓN

ESCALA: INDICADAS

FECHA 26 OCT 26


ALUMNO Fdo: Alejandro Gómez Jiménez

PLANO Nº 7


CUADRO DE PILARES Y ZAPATAS

REF.	ELEMENTO	DIMENSIONES	UDS.
P1-P13	Pilar	30 x 30 cm	13
Z1	Zapata aislada	90 x 90 cm	12
Z2	Zapata combinada	371 x 90 cm	1


Canto de zapatas y armado: según cálculo.

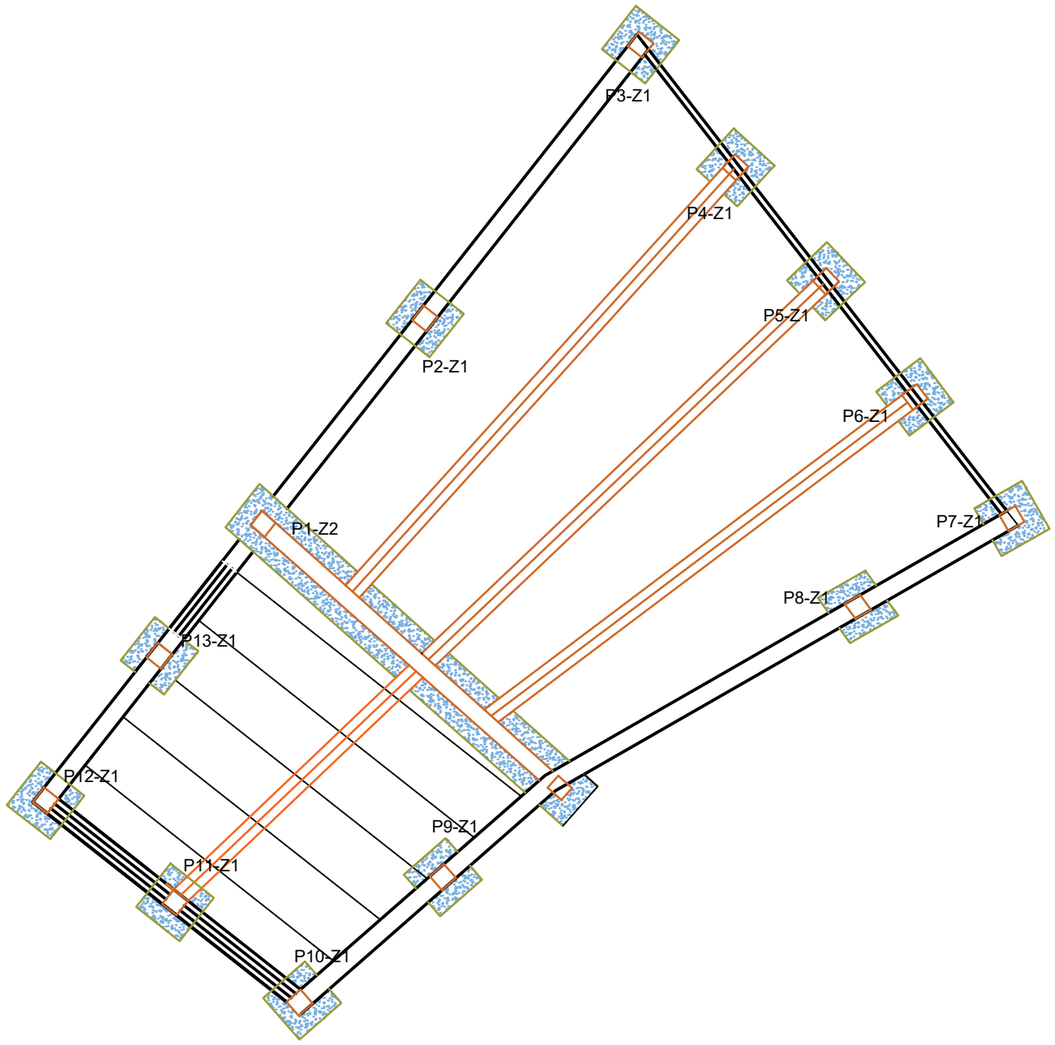

PLANTA DE CIMENTACIÓN
E 1:100

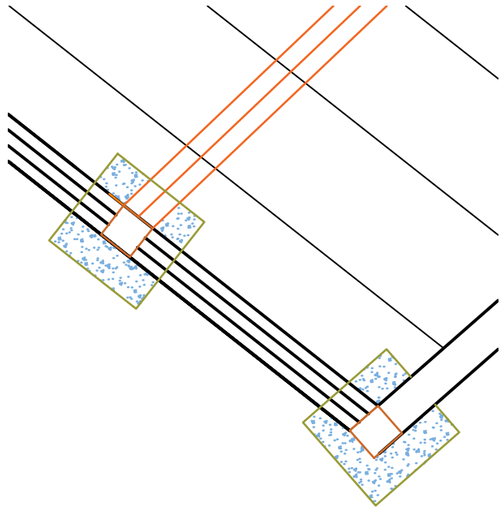

DETALLE ESQUINA
E 1:50

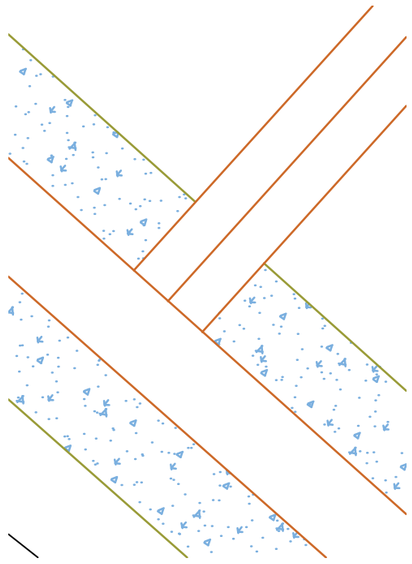

DETALLE PILAR-ZAPATA
E 1:20

CIMENTACIÓN
PROYECTO DE VIVIENDA UNIFAMILIAR
DANIEL
C.F.G.S. PROYECTOS DE EDIFICACIÓN
MÓDULO: REPRESENTACIONES DE CONSTRUCCIÓN

ESCALA: INDICADAS
FECHA 26 OCT 26
ALUMNO Fdo: Alejandro Gómez Jiménez
PLANO Nº 8