
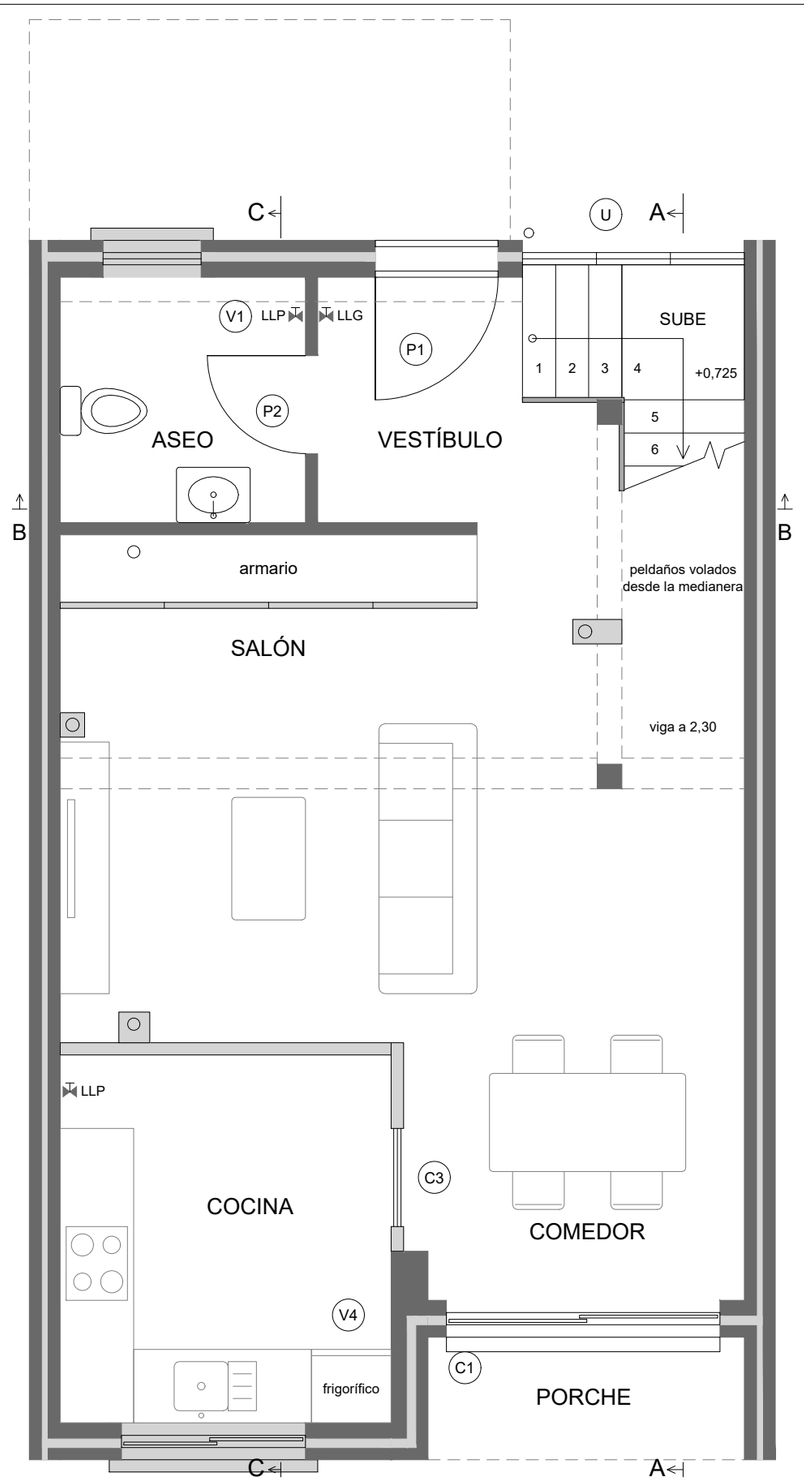



PLANTA BAJA · NPT ±0,00 · E 1:50

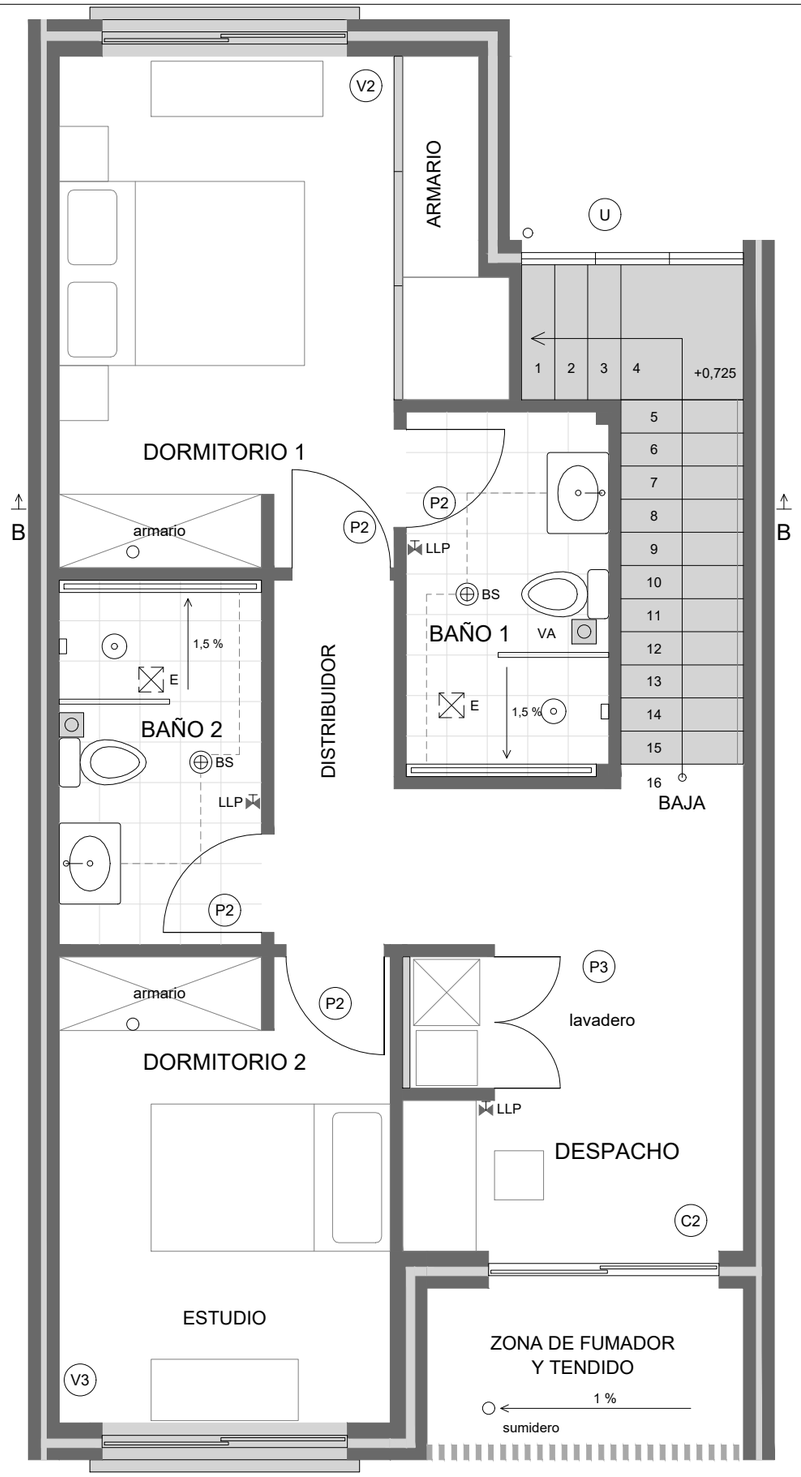

PLANTA PRIMERA · NPT +2,90 · E 1:50

LEYENDA

- BS bote sifónico registrable
- desagüe de lavabo y canaleta al bote
- LLP llave de paso del local húmedo
- LLG llave general de la vivienda
- canaleta lineal de ducha
- mampara de vidrio
- E extracción mecánica a cubierta
- bajante de residuales, forrada

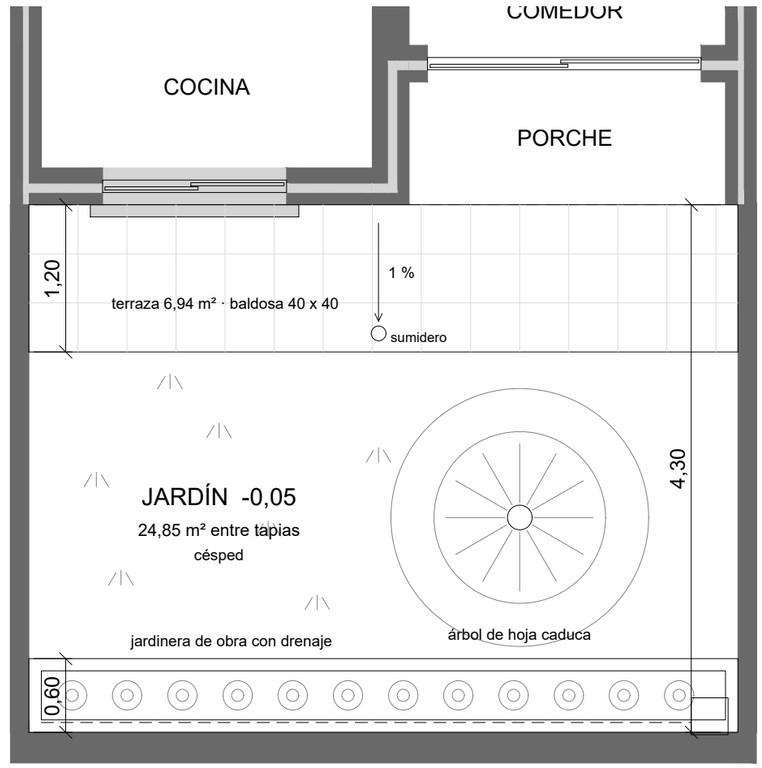

muro de contención · altura 1,45
tubo dren y arqueta al pie del muro
tapias h 2,00; sobre el muro, hasta +2,45

PLANTA DEL JARDÍN · E 1:50

I.E.S. AZARQUIEL
TOLEDO
C.F.G.S. PROYECTOS DE EDIFICACIÓN
MÓDULO: DESARROLLO DE PROYECTOS DE EDIFICACIÓN RESIDENCIAL

PROYECTO DE VIVIENDA UNIFAMILIAR

Vivienda piloto · tipo N · versión 2 · entre medianeras

Cotas en el plano 03; superficies en el 04; patios en el 12; cubierta en el 11; secciones en el 06, 07 y 10; detalles en el 08 (bote sifónico, D6). V, C, P, L y U: carpintería, plano 09. Discontinua: vigas y vuelos; bajo viga, altura libre 2,30. Pilares del hueco: HEB-140 revestido (predimensionado, a calcular). Tabiques de cocina de 1,10 con vidrio fijo hasta techo. VA: válvula de aireación de la bajante del baño 1. Mobiliario orientativo.

PLANO

DISTRIBUCIÓN

0 1 2 3 m

Plantas baja, primera y de jardín

ESCALA 1:50


FECHA NOV. 2026


PLANO Nº 02

ALUMNO
Fdo: Alejandro Gómez Jiménez

PROFESOR
Fdo: Juan Vicente de Torres Boada

N

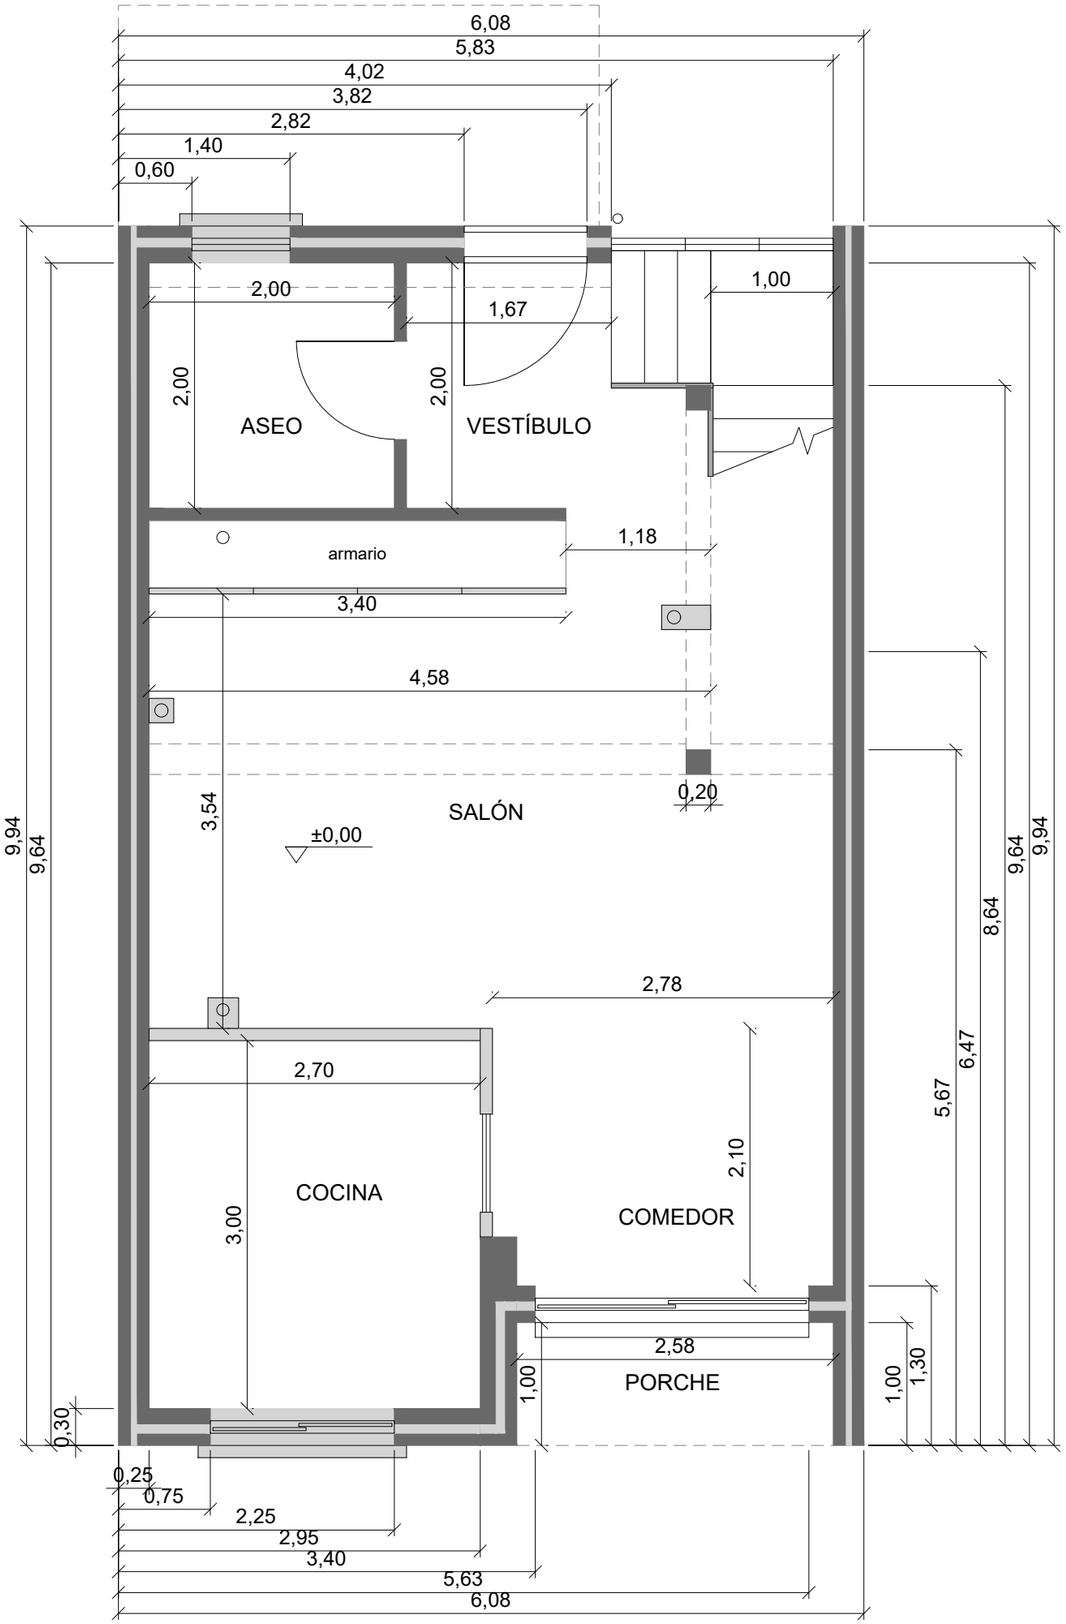

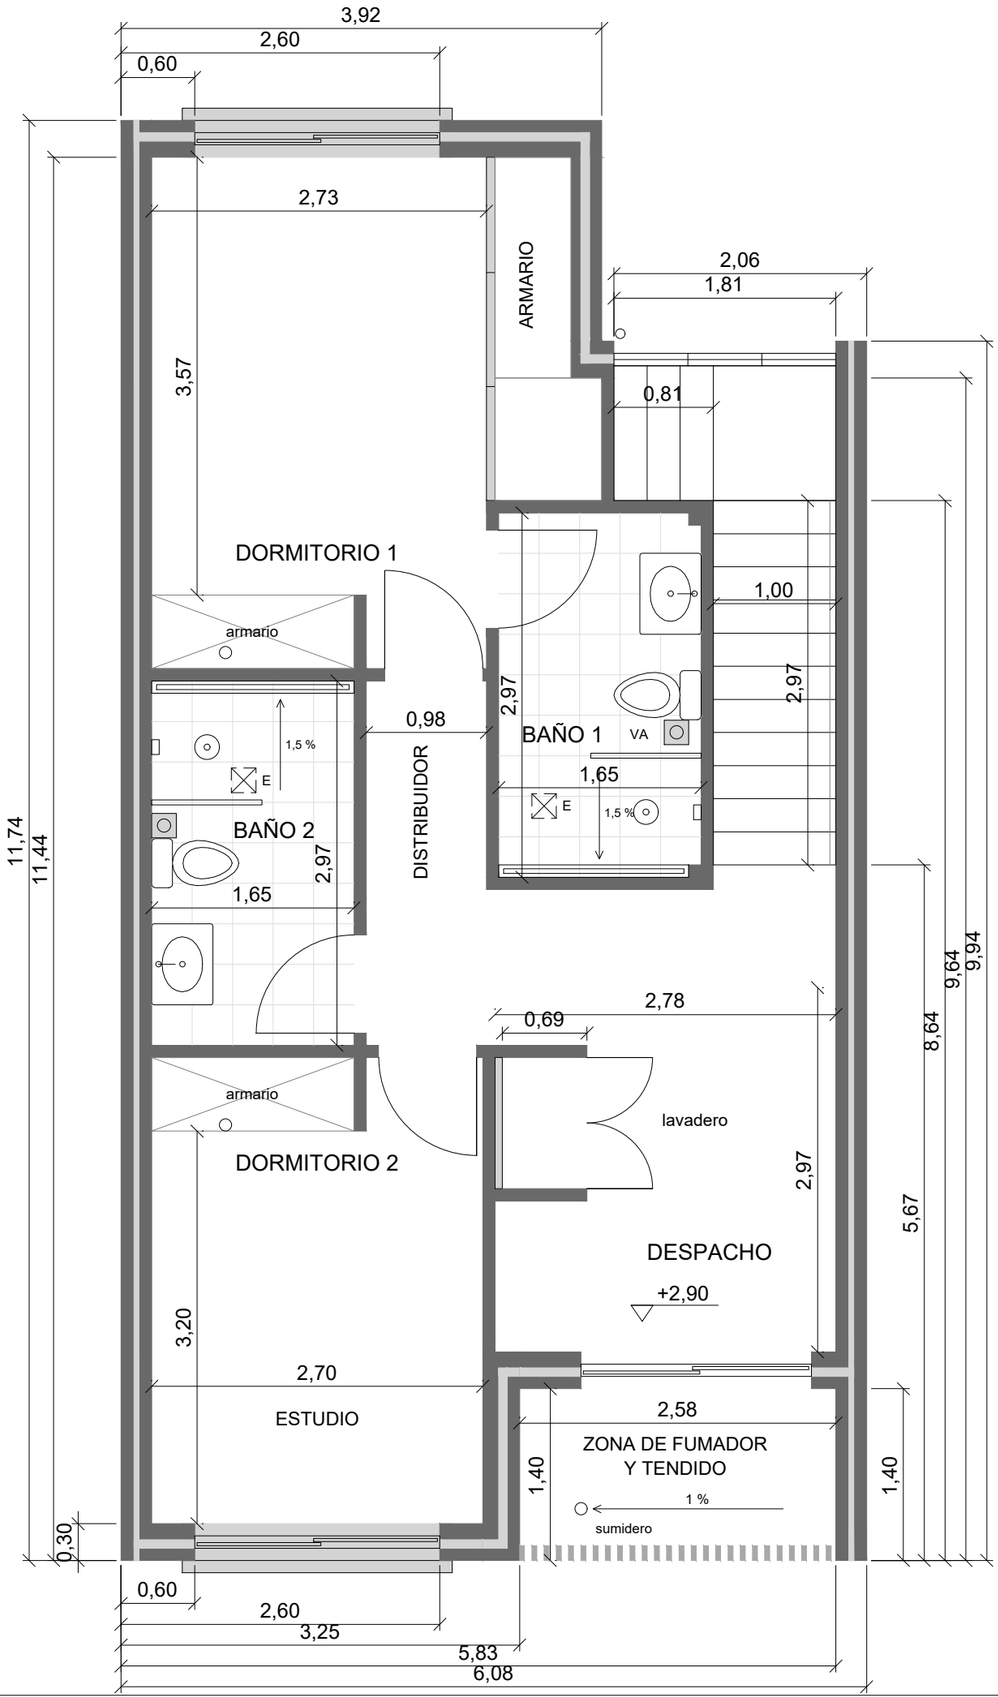

PLANTA BAJA · NPT ±0,00 · E 1:50

0 1 2 3 4 5 m

PLANTA PRIMERA · NPT +2,90 · E 1:50

I.E.S. AZARQUIEL
TOLEDO
C.F.G.S. PROYECTOS DE EDIFICACIÓN
MÓDULO: DESARROLLO DE PROYECTOS
DE EDIFICACIÓN RESIDENCIAL

PROYECTO DE VIVIENDA UNIFAMILIAR

Vivienda piloto · tipo N · versión 2

Entre medianeras · PB + P1 · parcela 6,08 m

NOTAS DE OBRA

1. Cotas en metros, a cara exterior de muro y a tabique terminado.
2. Medianeras 25 cm. Fachadas 30 cm: hoja exterior 10, aislamiento 7 e interior 13. Tabiques 10 cm.
3. Altura entre plantas 2,90 m (libre 2,60 m).
4. Comprobar las medidas en obra antes de ejecutar.

N

PLANO

COTAS

Plantas baja y primera · acotado para obra

ESCALA	FECHA
1:50	NOV. 2026

PLANO Nº


03


ALUMNO

Fdo: Alejandro Gómez Jiménez

PROFESOR

Fdo: Juan Vicente de Torres Boada

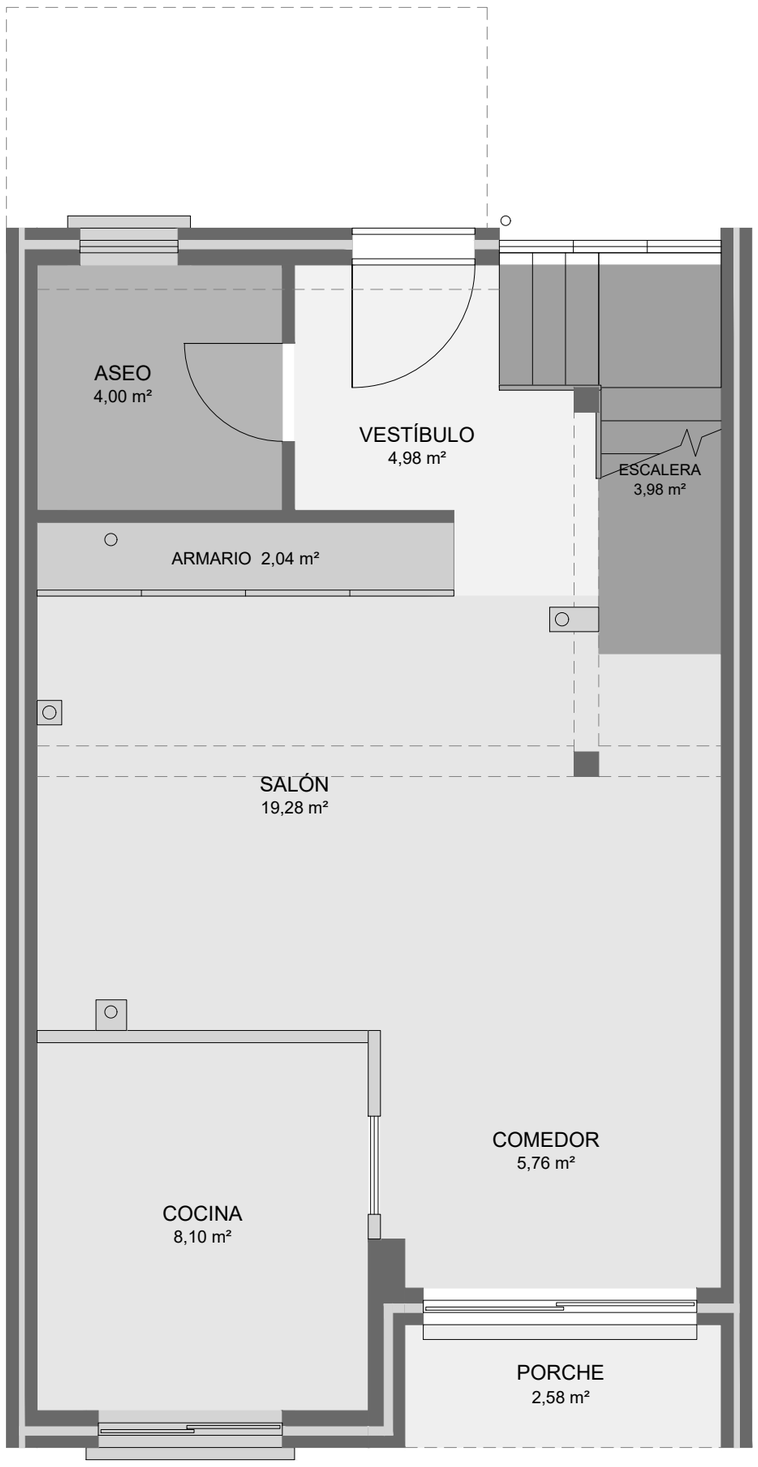

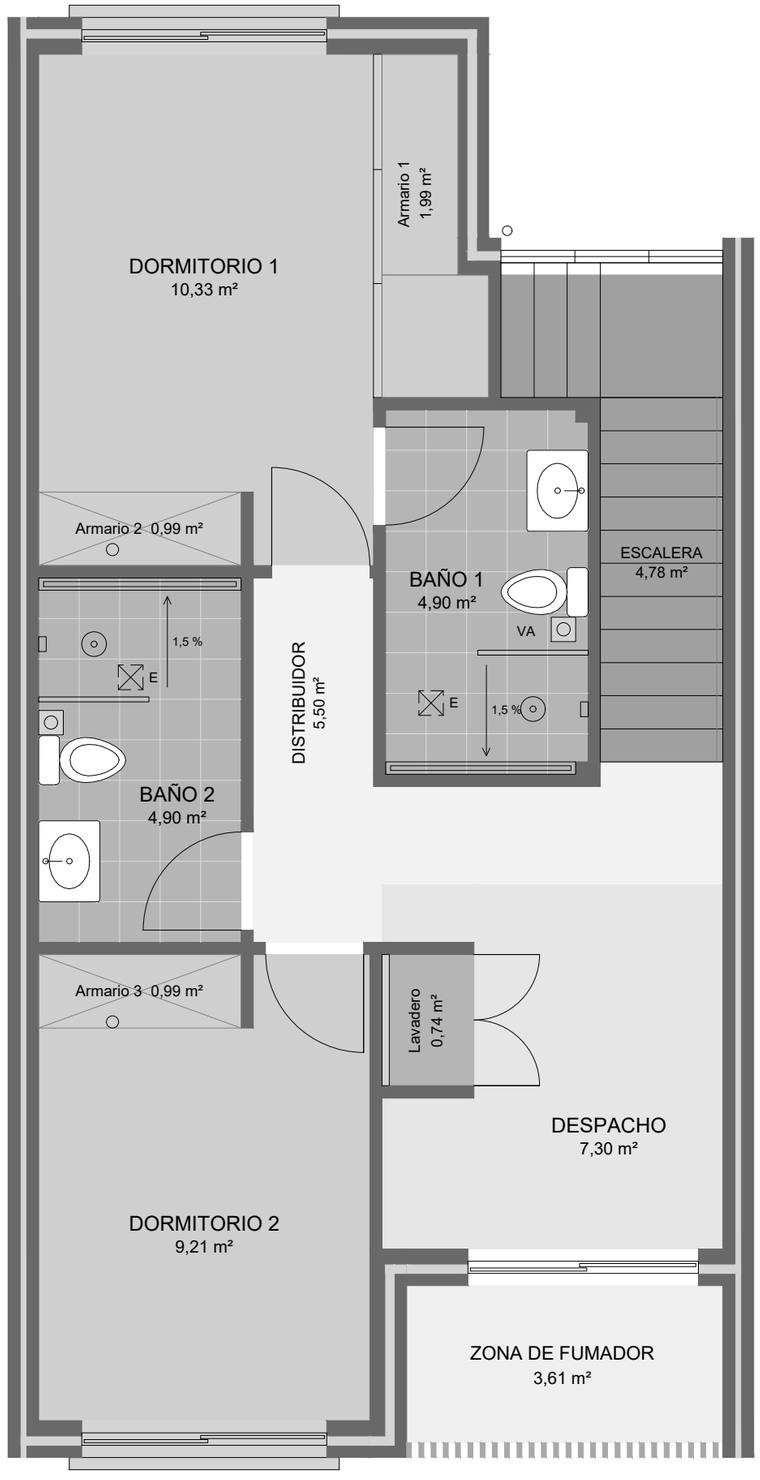

PLANTA BAJA · NPT ±0,00 · E 1:50 0 1 2 3 4 5 m PLANTA PRIMERA · NPT +2,90 · E 1:50

I.E.S. AZARQUIEL
TOLEDO

C.F.G.S. PROYECTOS DE EDIFICACIÓN
MÓDULO: DESARROLLO DE PROYECTOS
DE EDIFICACIÓN RESIDENCIAL

PROYECTO DE VIVIENDA UNIFAMILIAR

Vivienda piloto · tipo N · versión 2

Entre medianeras · PB + P1 · parcela 6,08 m

CUADRO DE SUPERFICIES ÚTILES

PLANTA BAJA	m²
Aseo	4,00
Vestíbulo	4,98
Salón	19,28
Comedor	5,76
Cocina	8,10
Armario	2,04
Escalera	3,98
Total útil planta baja	48,14
PLANTA PRIMERA	**m²**
Dormitorio 1	10,33
Armario 1	1,99
Armario 2	0,99
Baño 1	4,90
Baño 2	4,90
Distribuidor	5,50
Dormitorio 2	9,21
Armario 3	0,99
Despacho	7,30
Lavadero	0,74
Escalera	4,78
Total útil planta primera	51,63
TOTAL ÚTIL VIVIENDA	99,77

SUPERFICIES CONSTRUIDAS

Planta baja	57,86
Planta primera (con vuelos)	63,88
TOTAL CONSTRUIDA	121,74
Zona de fumador (no computa)	3,61
Porche (no computa)	2,58

ZONAS

Día · Noche · Húmedas · Circulación · Escalera · Exterior

N

PLANO

SUPERFICIES

Superficies útiles y construidas

ESCALA	FECHA
1:50	NOV. 2026

PLANO Nº


04

ALUMNO


Fdo: Alejandro Gómez Jiménez

PROFESOR

Fdo: Juan Vicente de Torres Boada

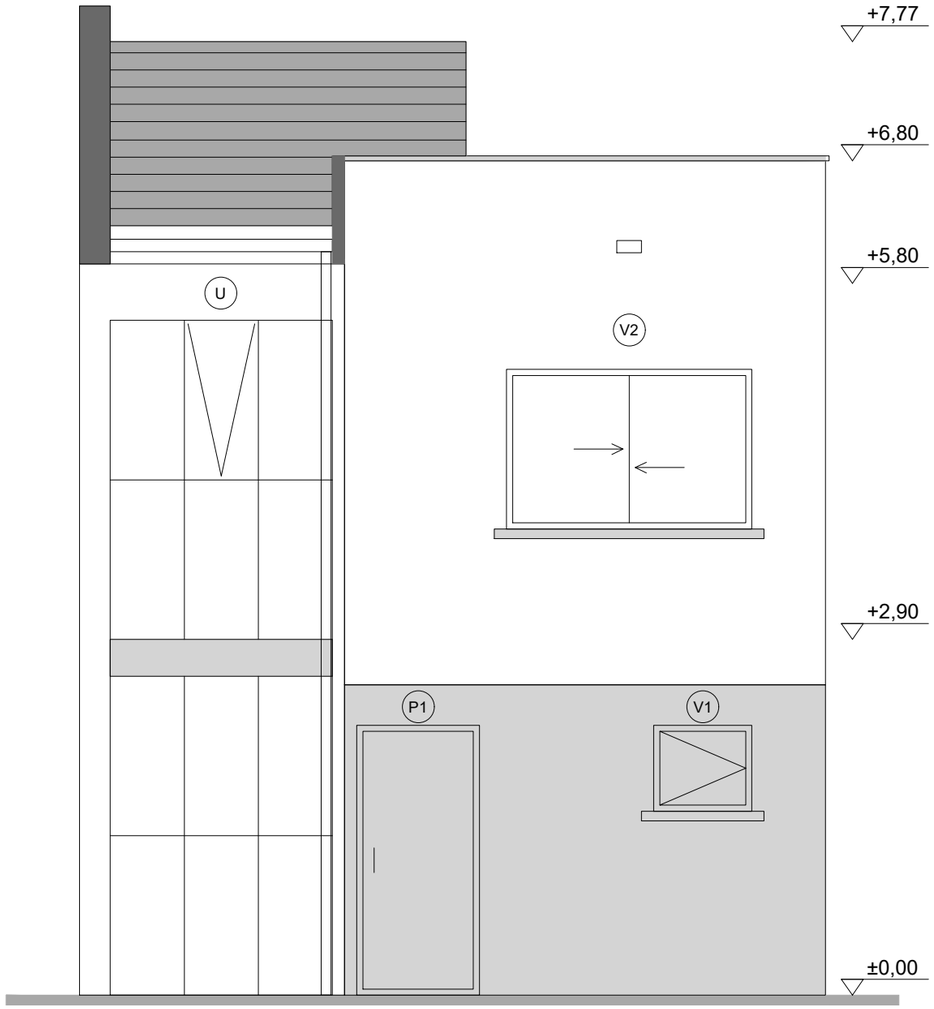

ALZADO NORTE (CALLE) · E 1:50

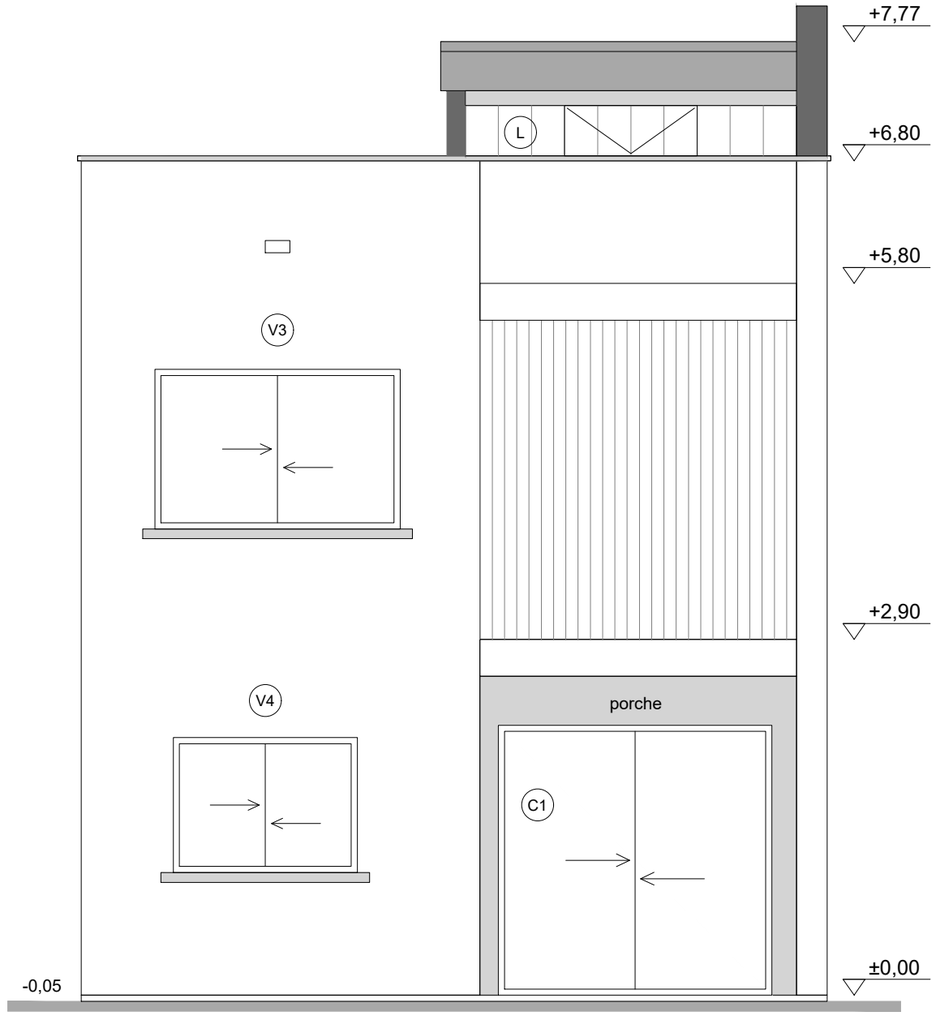

ALZADO SUR (JARDÍN) · E 1:50

I.E.S. AZARQUIEL
TOLEDO

C.F.G.S. PROYECTOS DE EDIFICACIÓN
MÓDULO: DESARROLLO DE PROYECTOS DE EDIFICACIÓN RESIDENCIAL

PROYECTO DE VIVIENDA UNIFAMILIAR

Vivienda piloto · tipo N · versión 2 · entre medianeras

Niveles en metros desde la calle norte (±0,00). Flechas: mecanismo de corredera. Triángulo: abatible. Tipos en el plano 09. Gris claro: planos en sombra, bajo vuelo.

PLANO

ALZADOS

0 1 2 3 m

Alzado norte (calle) y alzado sur (jardín)

ESCALA

1:50

FECHA

NOV. 2026

PLANO Nº

05

ALUMNO


Fdo: Alejandro Gómez Jiménez

PROFESOR

Fdo: Juan Vicente de Torres Boada



Clave de la sección A-A · E 1:200

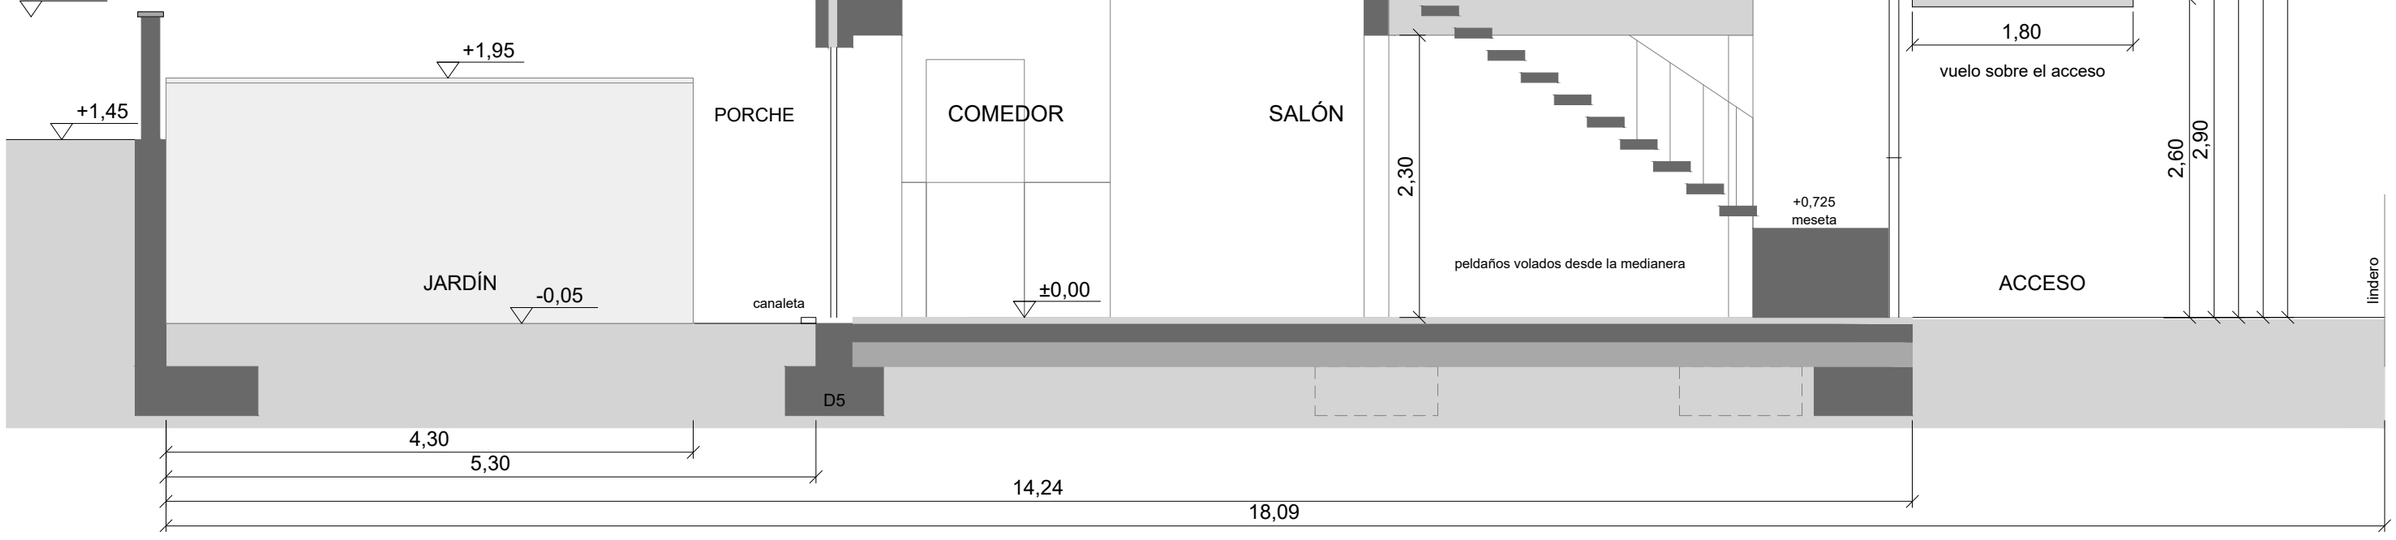

SECCIÓN A-A · E 1:50

I.E.S. AZARQUIEL
TOLEDO

C.F.G.S. PROYECTOS DE EDIFICACIÓN
MÓDULO: DESARROLLO DE PROYECTOS DE EDIFICACIÓN RESIDENCIAL

PROYECTO DE VIVIENDA UNIFAMILIAR

Vivienda piloto · tipo N · versión 2 · entre medianeras

Forjados de 30 cm. Altura libre 2,60 m. Escalera: 16 tabicas de 18,125 y 14 huellas de 27; tramo 1 y meseta de obra, tramo 2 volado desde la medianera (a calcular), barandilla de pletina. Lucernario de vidrio en U al sur: luz hasta la planta baja, con alero de sombra en verano. Muro de contención de 1,45 m al fondo. D1, D2, D4 y D5: plano 08.

PLANO

SECCIÓN A-A

0 1 2 3 m

Sección longitudinal por la escalera y el lucernario

ESCALA 1:50

FECHA NOV. 2026

PLANO Nº 06


ALUMNO
Fdo: Alejandro Gómez Jiménez

PROFESOR
Fdo: Juan Vicente de Torres Boada



Planta baja Planta primera Cubierta

Clave de la sección B-B · E 1:200

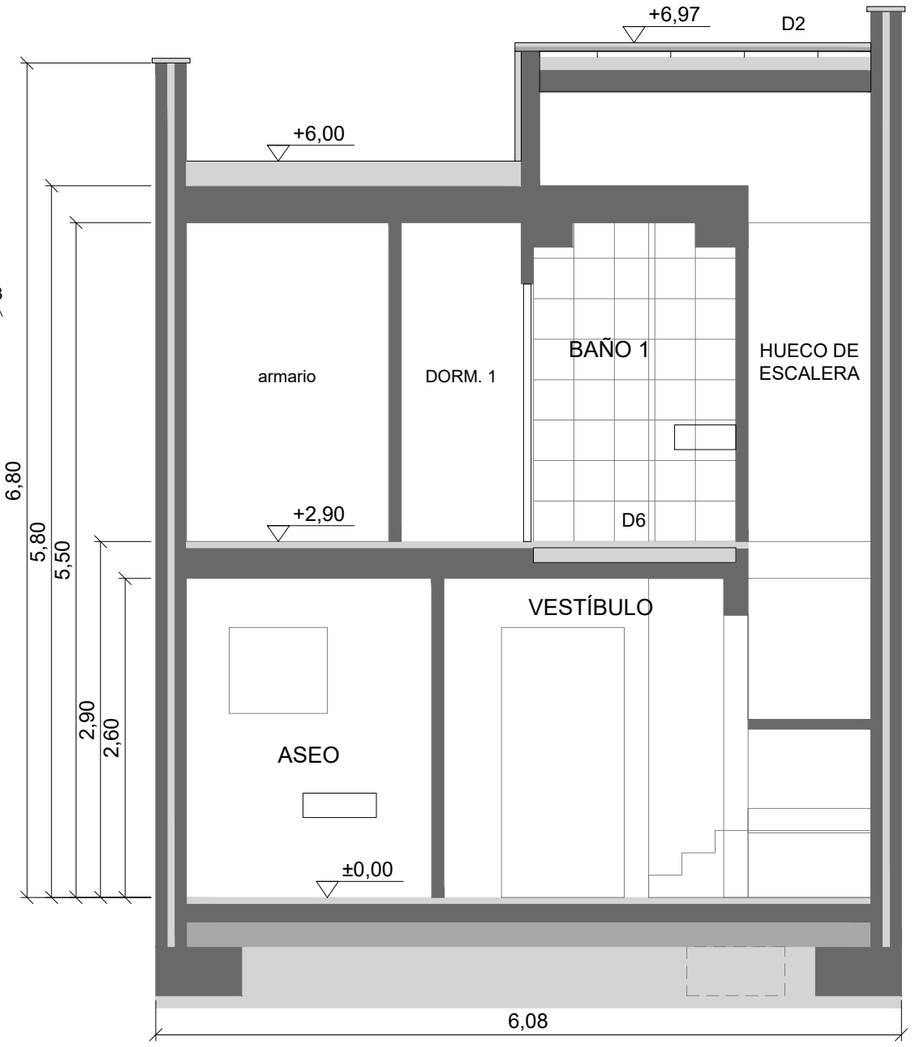


SECCIÓN B-B · E 1:50

I.E.S. AZARQUIEL TOLEDO C.F.G.S. PROYECTOS DE EDIFICACIÓN MÓDULO: DESARROLLO DE PROYECTOS DE EDIFICACIÓN RESIDENCIAL	PROYECTO DE VIVIENDA UNIFAMILIAR Vivienda piloto · tipo N · versión 2 · entre medianeras Sección por aseo, vestíbulo, baño 1 y hueco de escalera. Los baños son interiores: extracción mecánica a cubierta. D2 y D6: plano 08.	PLANO SECCIÓN B-B 0 1 2 3 m Sección transversal por aseo, vestíbulo, baño 1 y hueco de escalera	ESCALA 1:50 FECHA NOV. 2026	PLANO Nº 07	ALUMNO Fdo: Alejandro Gómez Jiménez PROFESOR Fdo: Juan Vicente de Torres Boada


D1 PETO Y CUBIERTA PLANA

E 1:10

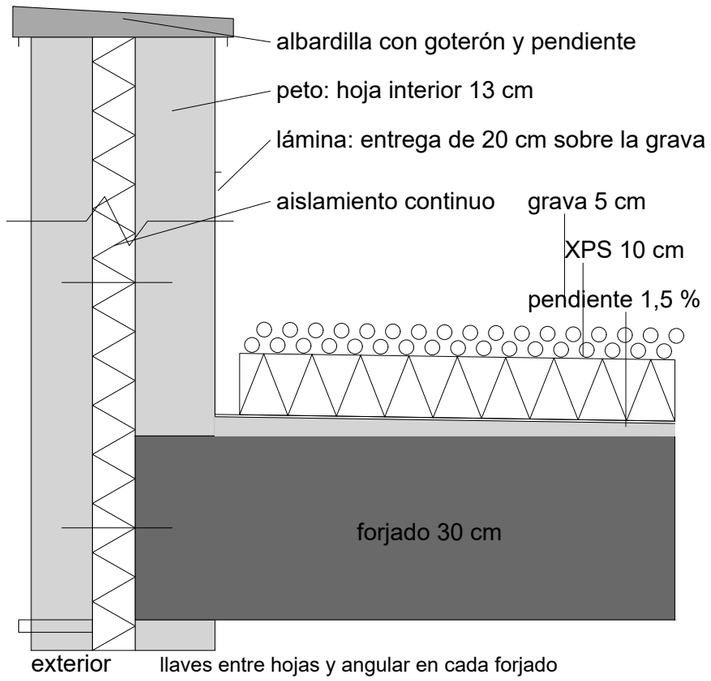


D2 CUBIERTA INCLINADA VENTILADA

E 1:10

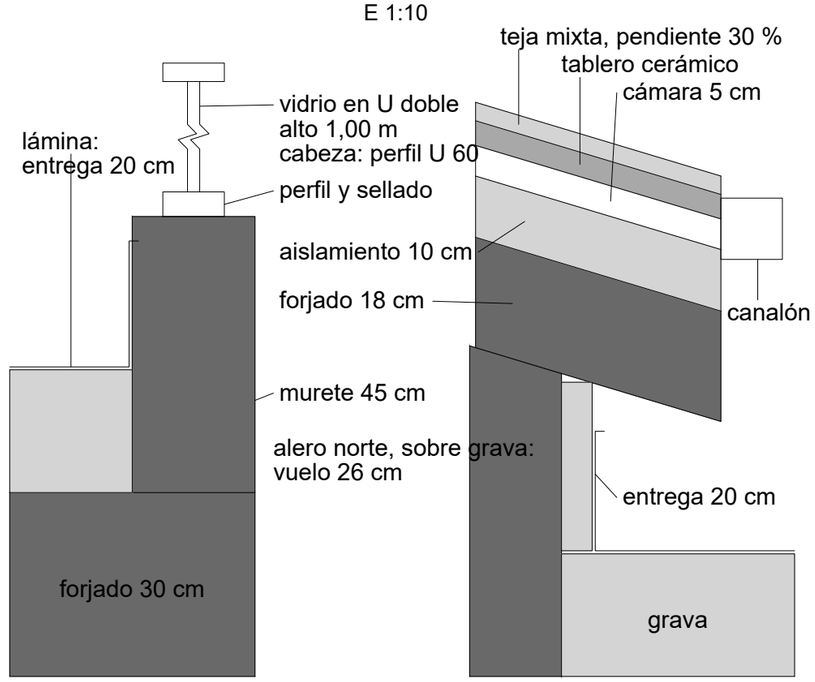


D3 VENTANA Y ALFÉIZAR

E 1:10

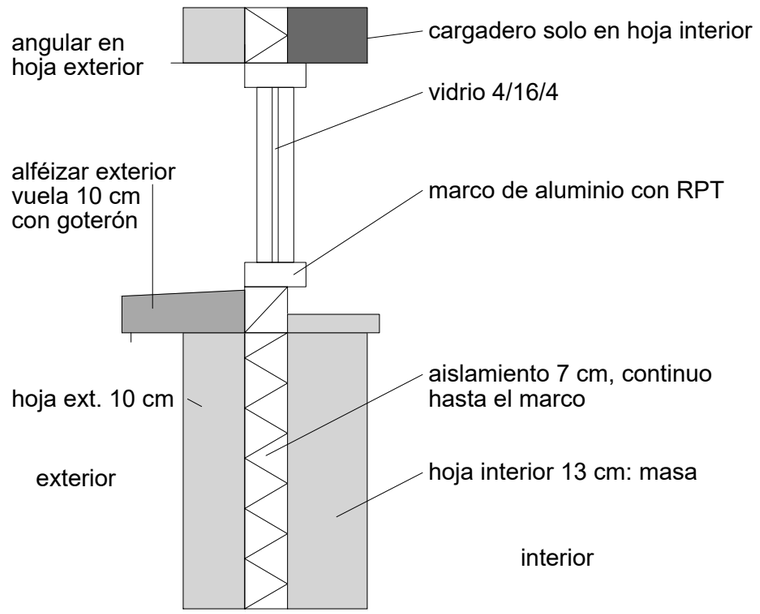


D4 LAMAS DE LA ZONA DE FUMADOR (PLANTA)

E 1:10

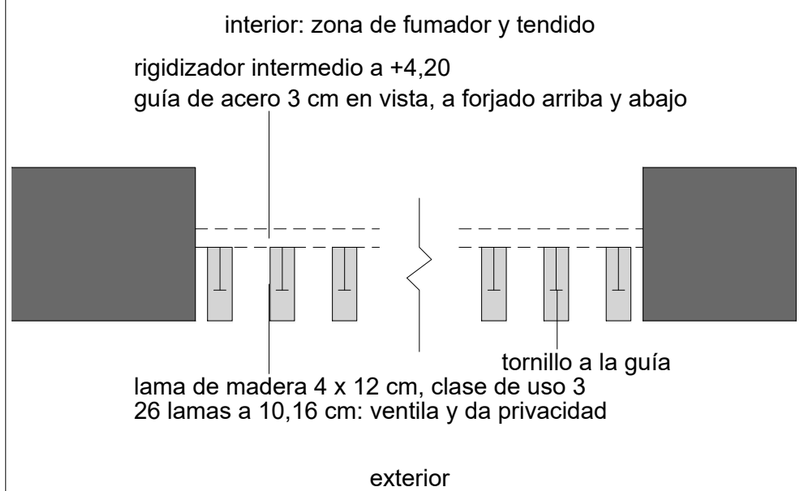

D5 CIMENTACIÓN Y SOLERA


E 1:10

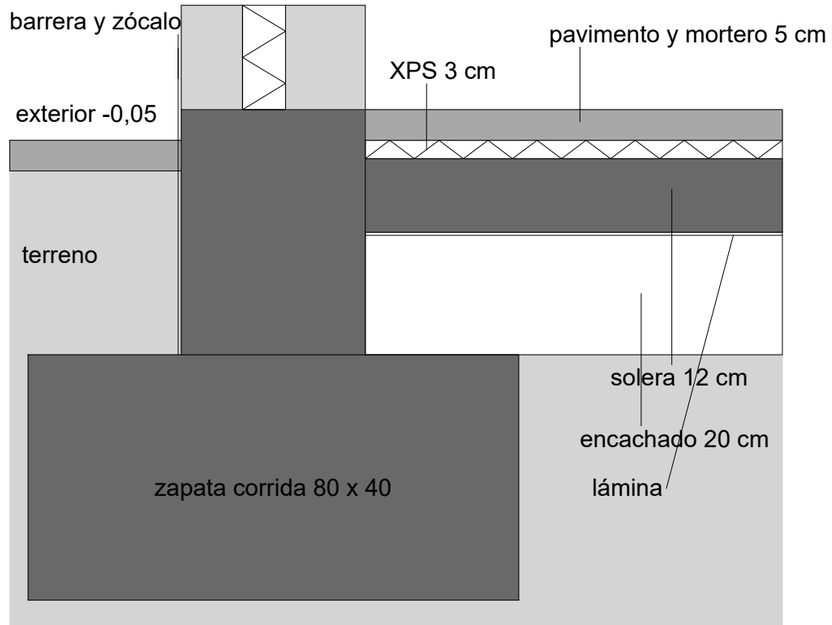

D6 SUELO HÚMEDO Y BOTE SIFÓNICO

E 1:10

Lavabo y canaleta van sin sifón propio: el cierre es el del bote

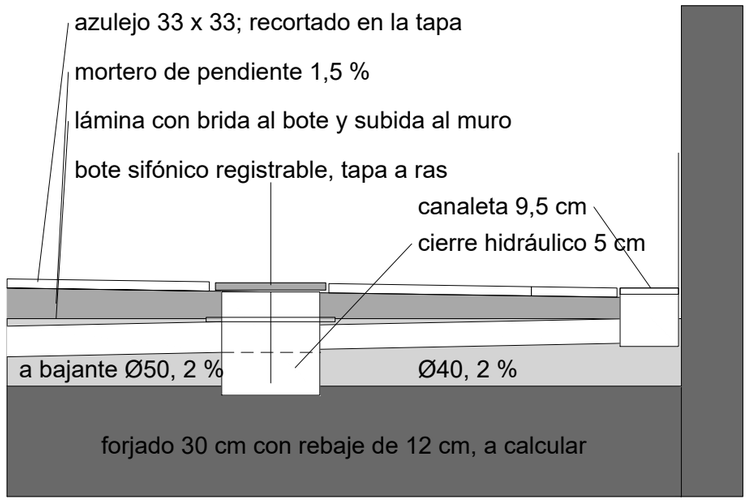

I.E.S. AZARQUIEL
TOLEDO

C.F.G.S. PROYECTOS DE EDIFICACIÓN
MÓDULO: DESARROLLO DE PROYECTOS DE EDIFICACIÓN RESIDENCIAL

PROYECTO DE VIVIENDA UNIFAMILIAR

Vivienda piloto · tipo N · versión 2 · entre medianeras

Muro de fachada con la masa por dentro del aislamiento: hoja exterior 10, aislamiento 7, hoja interior 13. Espesores a ajustar con el cálculo de estructura y el Código Técnico.

PLANO

DETALLES CONSTRUCTIVOS

0 0,1 0,2 0,3 0,4 0,5 m

Cubierta, lucernario, ventana, lamas, cimentación y baño

ESCALA

1:10

FECHA

NOV. 2026

PLANO Nº


08

ALUMNO

Fdo: Alejandro Gómez Jiménez


PROFESOR

Fdo: Juan Vicente de Torres Boada

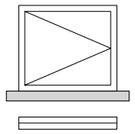


V1 Ventana del aseo

0,80 x 0,70 m
Abatible, 1 hoja
Aluminio con RPT, vidrio 4/16/4

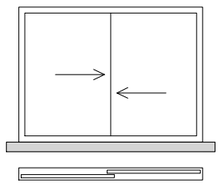


V4 Cocina, sobre la pila

1,50 x 1,10 m
Corredera, 2 hojas
Aluminio con RPT, vidrio 4/16/4

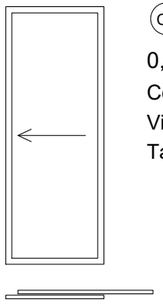


C3 Cocina a comedor

0,80 x 2,10 m
Corredera vista, hacia el comedor
Vidrio templado colgado de guía superior
Tabiques de 1,10 con vidrio fijo hasta techo

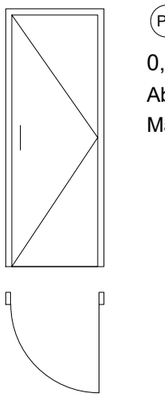


P2 Puertas interiores

0,80 x 2,10 m
Abatible, 1 hoja
Madera con tablero liso

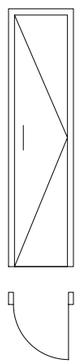


P3 Lavadero (x 2)

0,53 x 2,10 (x 2) m
Abatible, maciza con burlete
Reduce el ruido de la lavadora

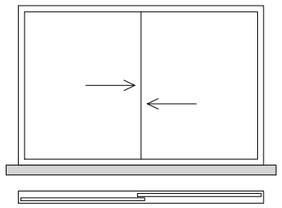


V2 Dormitorio 1

2,00 x 1,30 m
Corredera, 2 hojas
Aluminio con RPT, vidrio 4/16/4

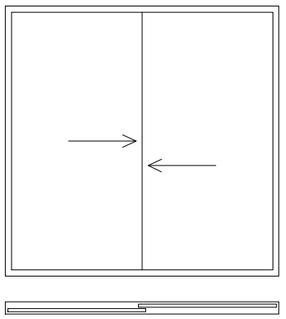


C1 Comedor a porche

2,23 x 2,20 m
Corredera, 2 hojas, a suelo
Aluminio con RPT, vidrio de seguridad

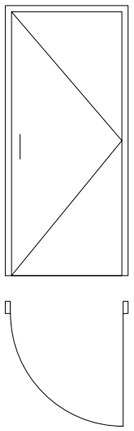


P1 Entrada

1,00 x 2,20 m
Abatible, acorazada
Madera y acero, con cerradura

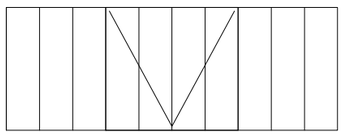


L Lucernario

2,70 x 1,00 m
Vidrio en U doble: 10 piezas de 0,27
Abatible de 1,08 con motor de cadena
Alero sur de 30 cm; pulsador en distribuidor

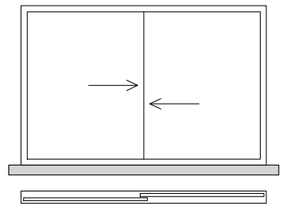


V3 Dormitorio 2

2,00 x 1,30 m
Corredera, 2 hojas
Aluminio con RPT, vidrio 4/16/4

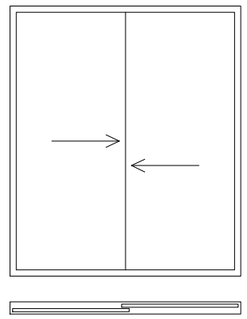

C2 Despacho a zona de fumador

1,88 x 2,20 m
Corredera, 2 hojas, a suelo
Aluminio con RPT, vidrio de seguridad

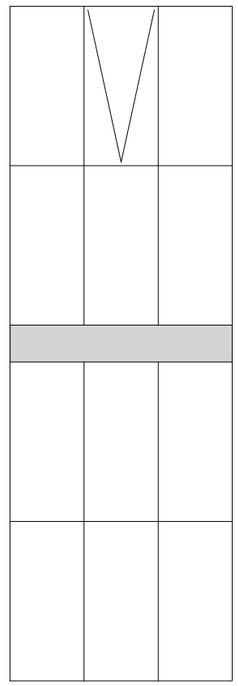

U Fachada de escalera

1,81 x 5,50 m
12 piezas de 0,60 x 1,30; alta central abatible
Doble bajo emisivo 6/16/4+4 traslúcido, con RPT
Abajo, laminar de seguridad: protege la meseta
Abatible con motor de cadena; pulsador en distribuidor
Travesaño opaco +2,60/+2,90: tubo de acero y panel

I.E.S. AZARQUIEL
TOLEDO

C.F.G.S. PROYECTOS DE EDIFICACIÓN
MÓDULO: DESARROLLO DE PROYECTOS DE EDIFICACIÓN RESIDENCIAL

PROYECTO DE VIVIENDA UNIFAMILIAR

Vivienda piloto · tipo N · versión 2 · entre medianeras

Medidas de hueco en metros; comprobar en obra antes de fabricar. Todas las ventanas llevan alféizar exterior con el aislamiento continuo hasta el marco (detalle D3). Puertas y correderas a suelo sin alféizar.

PLANO

CARPINTERÍA

0 1 2 3 m

Tipos, medidas y mecanismos


ESCALA
1:50

FECHA
NOV. 2026


PLANO Nº
09

ALUMNO
Fdo: Alejandro Gómez Jiménez

PROFESOR
Fdo: Juan Vicente de Torres Boada

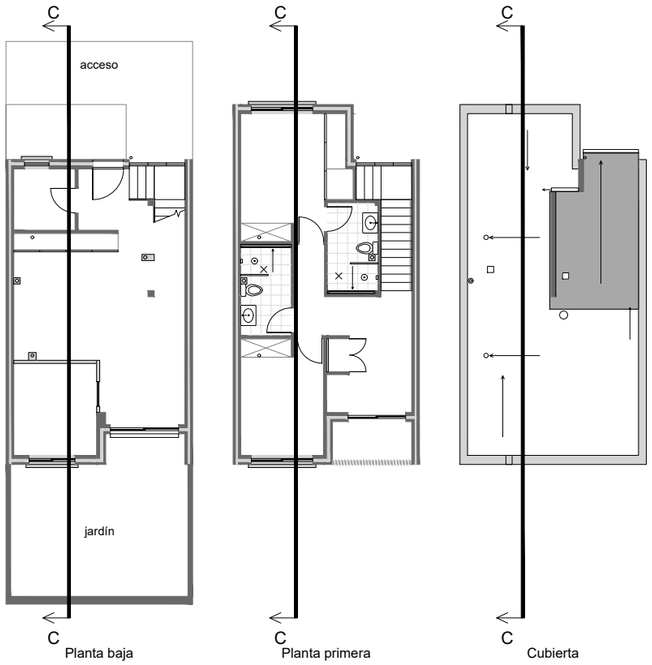

Clave de la sección C-C · E 1:200

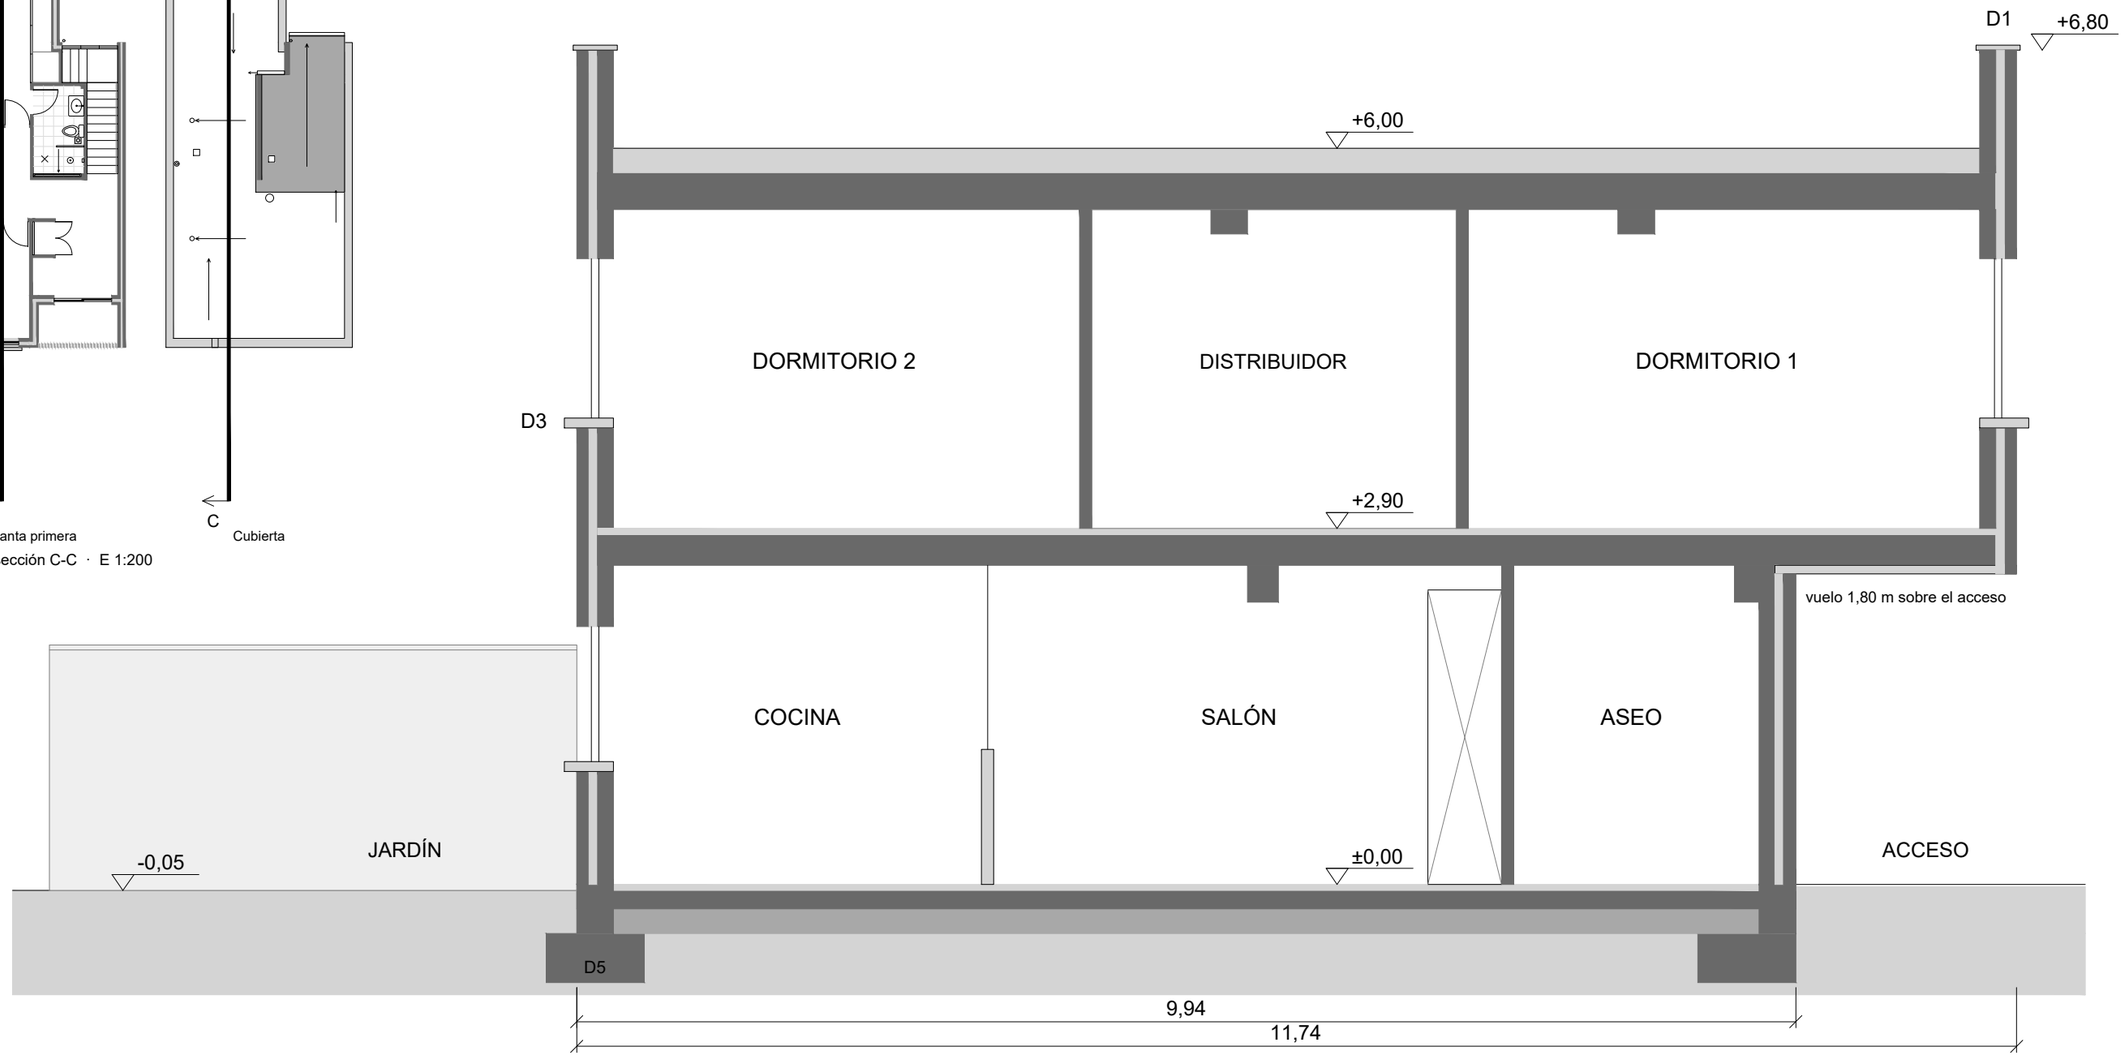

SECCIÓN C-C · E 1:50

I.E.S. AZARQUIEL
TOLEDO
C.F.G.S. PROYECTOS DE EDIFICACIÓN
MÓDULO: DESARROLLO DE PROYECTOS DE EDIFICACIÓN RESIDENCIAL

PROYECTO DE VIVIENDA UNIFAMILIAR

Vivienda piloto · tipo N · versión 2 · entre medianeras

Muestra el vuelo de 1,80 m sobre el acceso y su viga de apoyo en la fachada norte. Niveles en metros. D1, D3 y D5: plano 08.

PLANO

SECCIÓN C-C

0 1 2 3 m

Sección longitudinal por el volado norte

ESCALA

1:50

FECHA

NOV. 2026

PLANO Nº


10

ALUMNO

Fdo: Alejandro Gómez Jiménez

PROFESOR

Fdo: Juan Vicente de Torres Boada

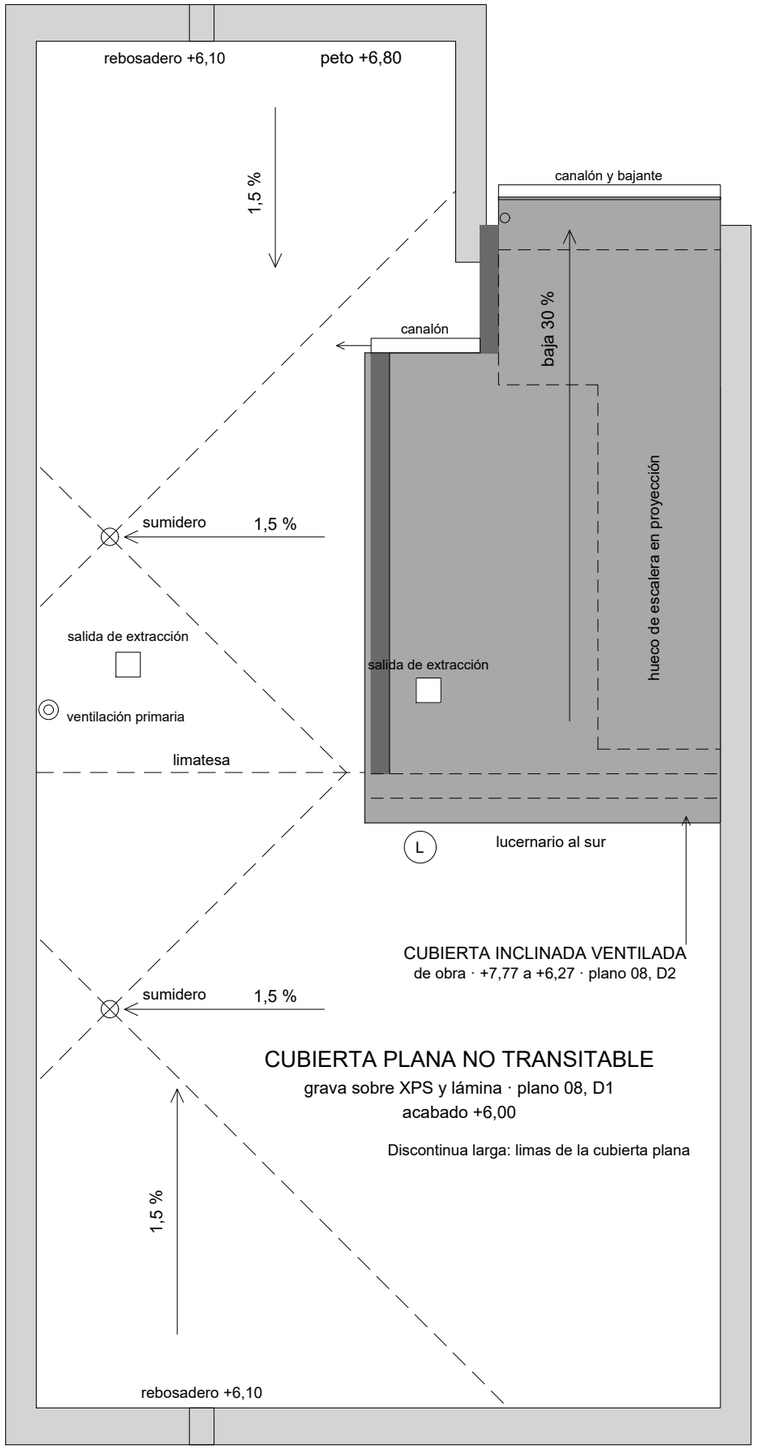

PLANTA DE CUBIERTA · E 1:50

I.E.S. AZARQUIEL
TOLEDO

C.F.G.S. PROYECTOS DE EDIFICACIÓN
MÓDULO: DESARROLLO DE PROYECTOS DE EDIFICACIÓN RESIDENCIAL

PROYECTO DE VIVIENDA UNIFAMILIAR

Vivienda piloto · tipo N · versión 2 · entre medianeras

Cubierta plana no transitable de grava y cubierta inclinada de obra ventilada. Encuentros en el plano 08 (D1 y D2). Secciones en el 06, 07 y 10. Lucernario de vidrio en U al sur: tipo L, plano 09.

PLANO

PLANTA DE CUBIERTA

0 1 2 3 m

Cubierta plana y cubierta inclinada ventilada

ESCALA
1:50

FECHA
NOV. 2026

PLANO Nº
11


ALUMNO
Fdo: Alejandro Gómez Jiménez

PROFESOR
Fdo: Juan Vicente de Torres Boada

N




PATIO DE ACCESO (NORTE) · E 1:50

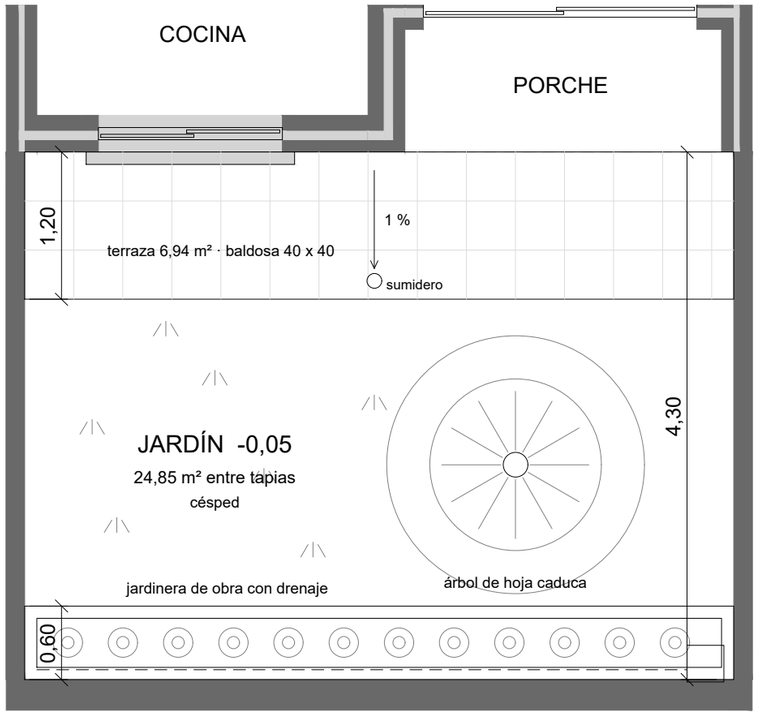

muro de contención · altura 1,45
tubo dren y arqueta al pie del muro
tapias h 2,00; sobre el muro, hasta +2,45

JARDÍN (SUR) · E 1:50

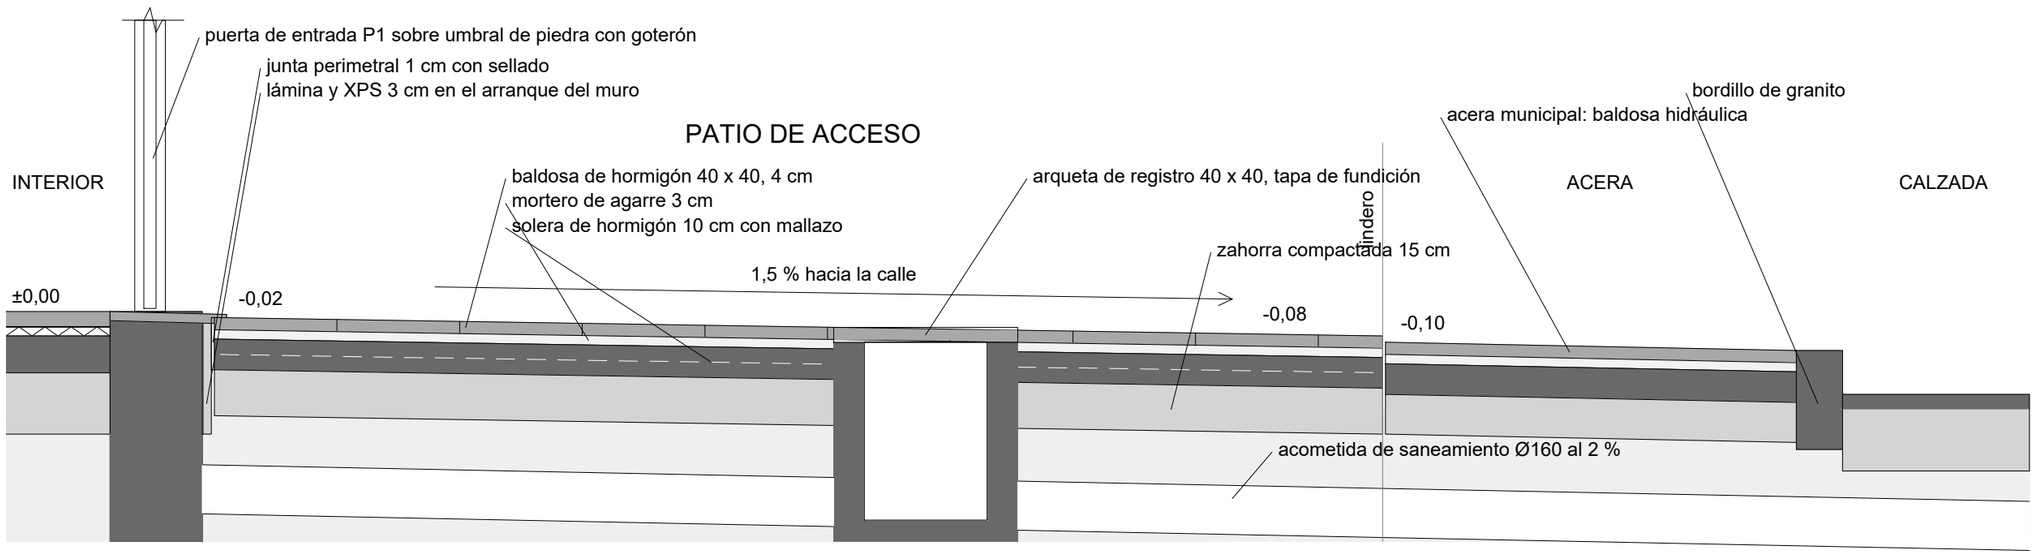

DETALLE CONSTRUCTIVO DEL PATIO DE ACCESO, POR LA PUERTA DE ENTRADA · E 1:20

I.E.S. AZARQUIEL
TOLEDO
C.F.G.S. PROYECTOS DE EDIFICACIÓN
MÓDULO: DESARROLLO DE PROYECTOS DE EDIFICACIÓN RESIDENCIAL

PROYECTO DE VIVIENDA UNIFAMILIAR

Vivienda piloto · tipo N · versión 2 · entre medianeras

Pavimento exterior de baldosa de hormigón 40 x 40 sobre solera, con pendiente hacia la calle y hacia el jardín. Jardinera de obra ante el vidrio de la escalera. Muro de contención con tubo dren al pie y arqueta. Árbol de hoja caduca: sombra en verano, sol en invierno.

PLANO

PATIOS

Patio de acceso y jardín: superficies, pavimentos, plantación y drenaje

ESCALA
VARIAS

FECHA
NOV. 2026

PLANO Nº
12

ALUMNO
Fdo: Alejandro Gómez Jiménez

PROFESOR
Fdo: Juan Vicente de Torres Boada

N